


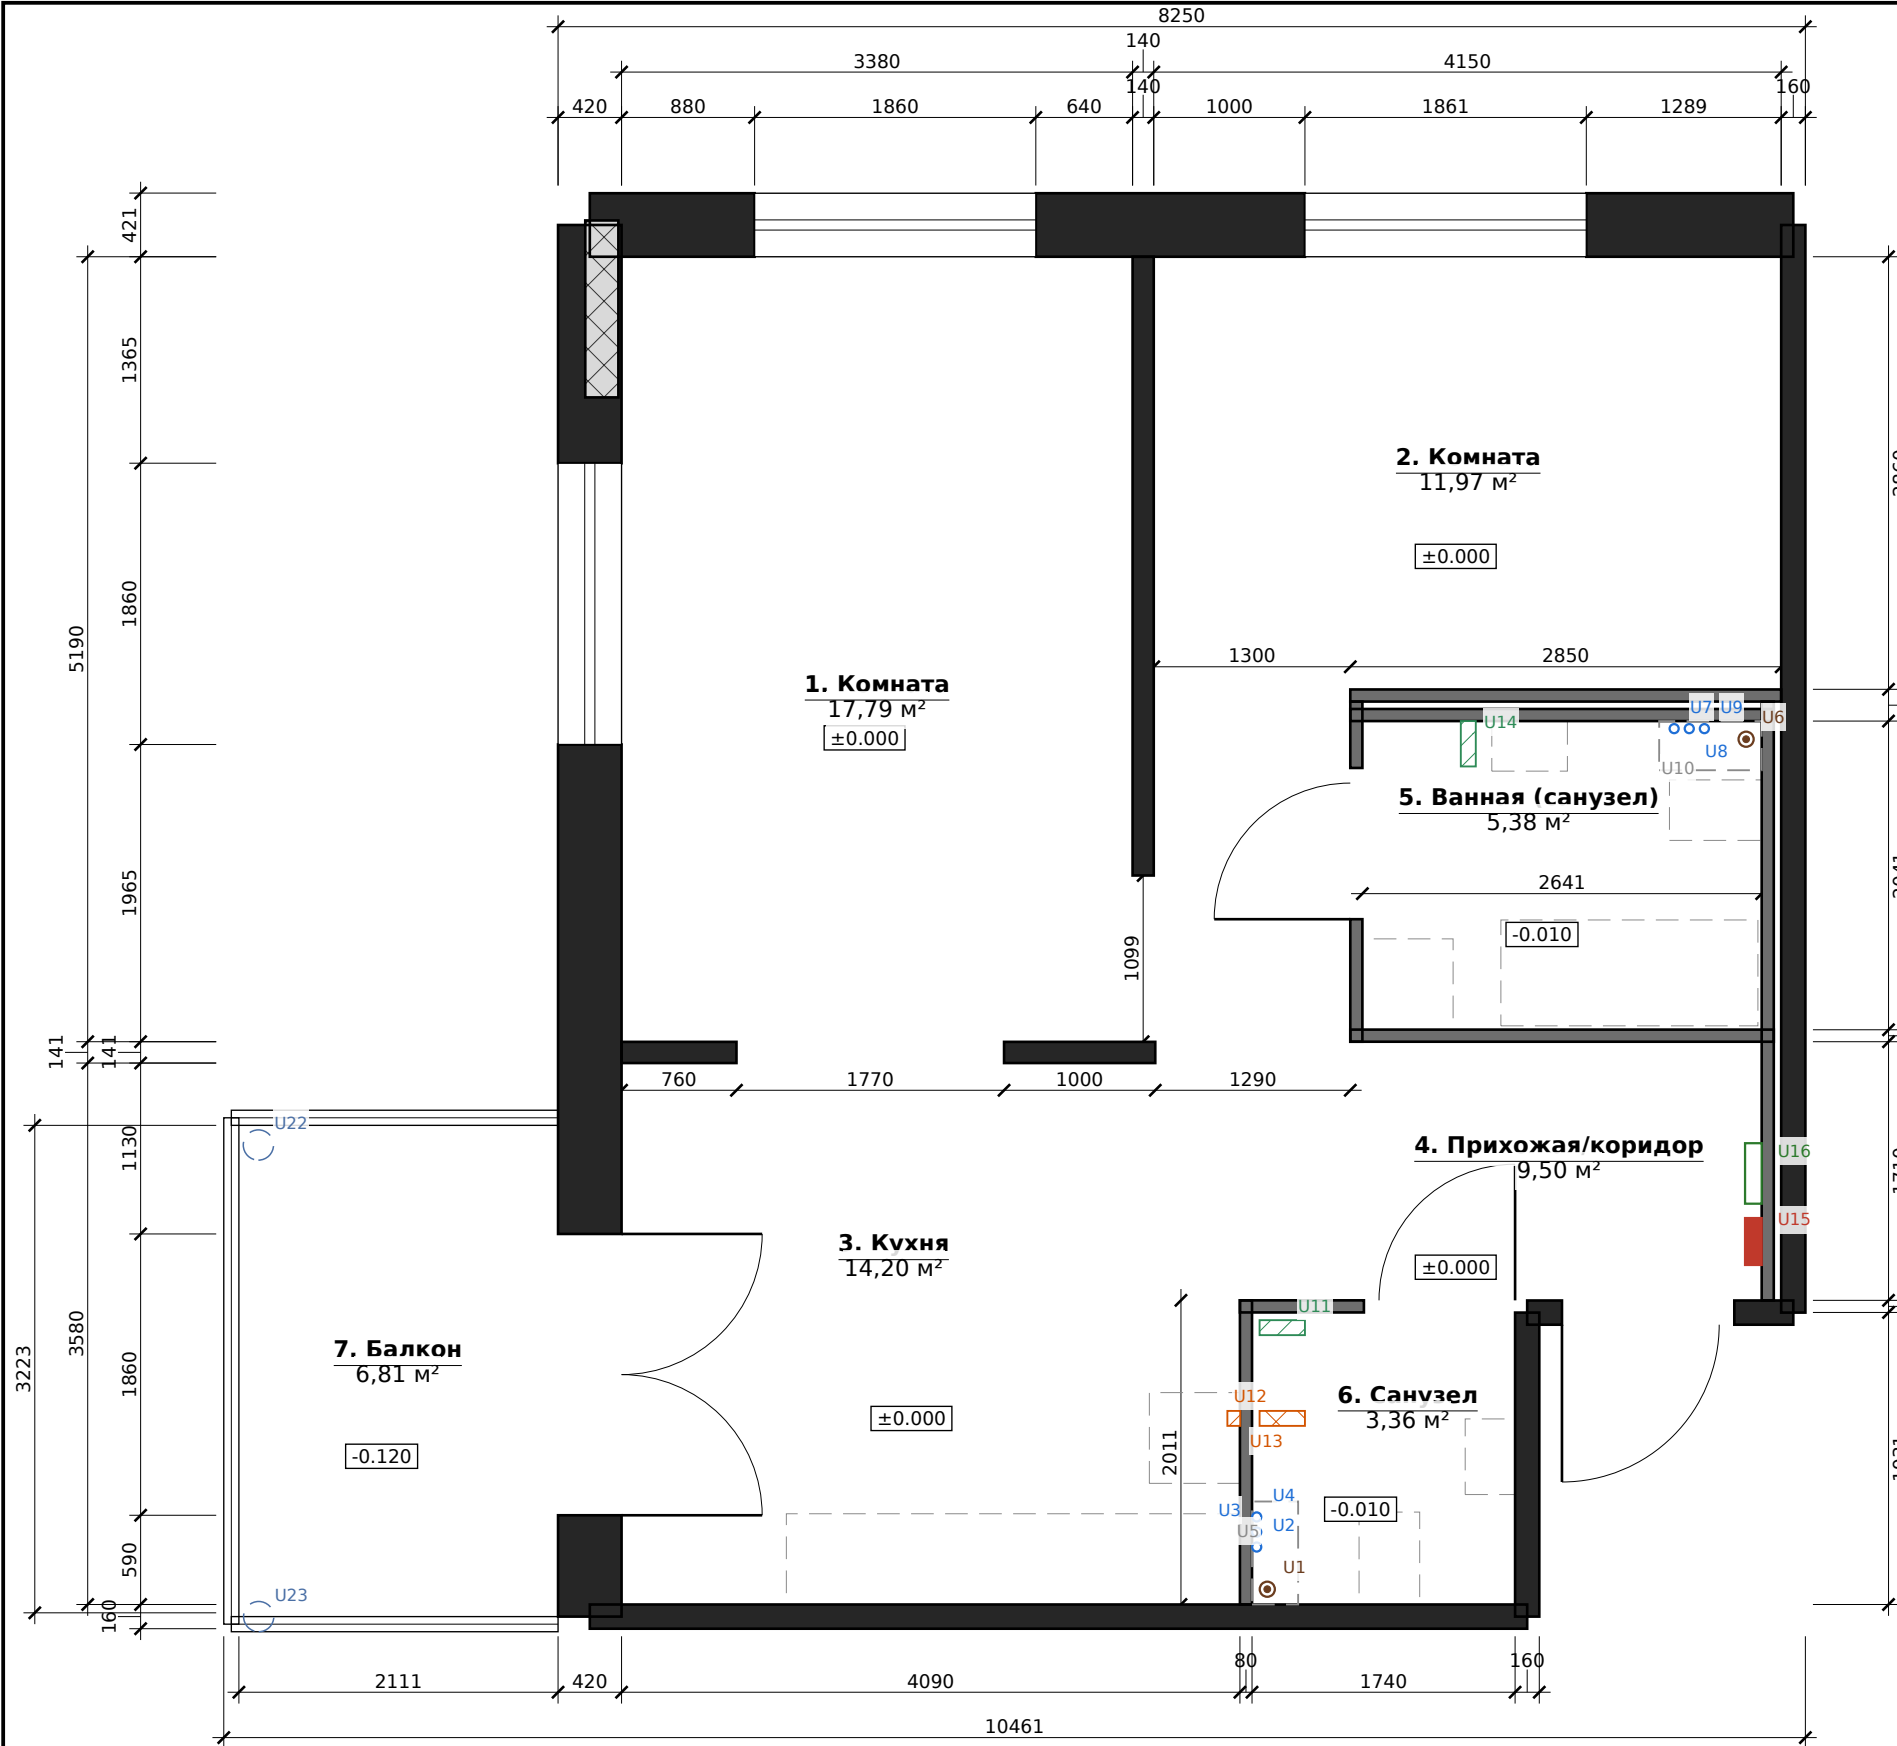

- Условные обозначения**
- Несущие и наружные стены (по плану застройщика)
 - Перегородки застройщика 80
 - Ж/б колонна С1 (не трогать)
 - Стояк канализации К1
 - Стояк водоснабжения (В1/Т3/Т4 — уточнить)
 - Короб стояков
 - Вентканал / решётка
 - Коллектор водяного ТП (h=400)
 - Щит ЭЩ (U15), [допущение]
 - Приборы застройщика (условно)

Привязки инженерных точек (центр)		
Марка	Тип	Привязка к границам стен, мм
U1	riser_sewer	101 от W10; 101 от W3
U2	riser_water	31 от W10; 380 от W3
U3	riser_water	31 от W10; 479 от W3
U4	riser_water	31 от W10; 579 от W3
U5	riser_box	152 от W10; 340 от W3
U6	riser_sewer	103 от W14; 120 от W15
U7	riser_water	579 от W14; 50 от W15
U8	riser_water	479 от W14; 50 от W15
U9	riser_water	379 от W14; 50 от W15
U10	riser_box	339 от W14; 163 от W15
U11	ufh_manifold	200 от W10; 101 от W11
U12	vent_shaft	200 от W10; 701 от W11
U13	vent_grille	40 от W10; 1230 от W3
U14	ufh_manifold	700 от W12; 150 от W15
U15	el_panel	0 от W14; 390 от W5
U16	lowcurrent_panel	0 от W14; 840 от W5
U22	balcony_post_or_drain	129 от B1; 130 от B2
U23	balcony_post_or_drain	131 от B1; 0 от B3
U25	vent_shaft	152 от W10; 340 от W3
U26	vent_shaft	339 от W14; 163 от W15

Проёмы (низ/верх от УЧП)					
Проём	Стена	Участок	Ш	Низ	Верх
O1	W2	5686..7546	1860	850	2450
O2	W1	880..2740	1860	850	2450
O3	W1	4520..6381	1860	850	2450
O4	W2	590..2450	1860	0	2450
O5	W5	6220..7360	1140	0	2100
O6	W11	4910..5910	1000	0	2100
O7	W12	4531..5531	1000	0	2100
O8	W7	3721..4820	1099	0	2750
O9	W8	760..2530	1770	0	2750

Примечания

1. Размеры — по векторному PDF застройщика (14,9745 мм/pt), без фактического обмера: все размеры уточнить по месту.
2. ±0.000 = УЧП = верх плиты +100; низ плиты перекрытия +2.750.
3. Отметки пола и верх проёмов — [ДОПУЩЕНИЯ] measurement.json.

						КВ108-ДП-АР-01			
						Квартира №108, СПб, дизайн-проект			
Изм.	Кол.уч	Лист	№док.	Подп.	Дата	Архитектурные решения	Стадия	Лист	Листов
Разраб.		риб-агенты			10.2026		Р	5	51
Пров.									
ГИП									
Н.контр.						Обмерный план Масштаб 1:50	ПИБ агенты риб-*		
Утв.									