


Вариант А — «Минимальное вмешательство»: санузел в существующих стенах — М 1:100

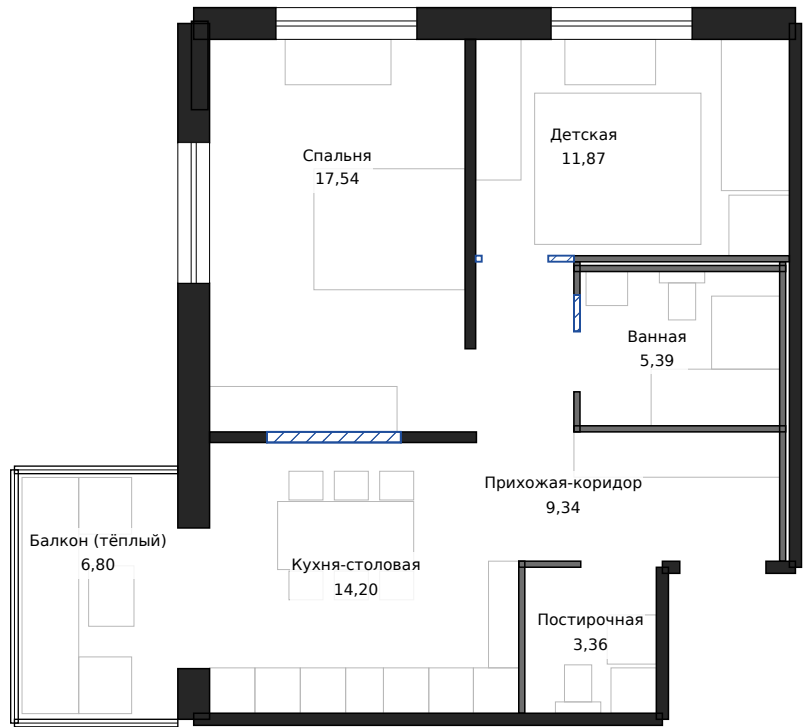

Все мокрые зоны — в существующих границах. Спальня 17,79 изолируется закладкой проёма О9 и дверью в существующем проёме О8, гардероб — встроенный шкаф 2480×600 вдоль заложённого проёма. Детская 11,97 закрывается перегородкой с дверью. Основной санузел 2640×2040 вмещает ванну 1700, walk-in душ 900×966, сантехнику и раковину 550 — с минимальными проходами 650 мм; дверь ванной смещается вниз по W12. Постирочная — с гостевым унитазом, дверь О6 сохраняется.

Плюсы: минимум работ и согласований: мокрые зоны в существующих границах; коридор сохраняет ширину 1300; шкаф 2480×600 в спальне без дополнительных перегородок; простая геометрия спальни 17,5 м²; постирочная с гостевым WC и дверью застройщика

Минусы: ванная на пределе: проход между ванной и унитазом 650, раковина 550, вход в душ сбоку 650 — без места под хранение; нет гардеробной (шкаф 2480 п.м. — минимум программы); в постирочной нет высокого шкафа (зона двери О6 900) — пылесос/гладильная доска в шкафу прихожей; кровать изголовьем к W7 — смежной стене с детской

Вариант В — «Комфортный санузел + гардеробная» [РЕКОМЕНДОВАН] — М 1:100



Основной санузел расширяется на 290 мм за счёт коридора (коридор 1300 -> 1000, норма ≥ 850): 2920×2040 = 5,96 м² — ванна 1700, walk-in душ у стояка, сантехника, тумба 800, шкаф; дверь ванной — у прихожей. Спальня 17,79 делится лёгкими перегородками на спальную зону (13,0 м², два окна) и гардеробную 4,2 м² без окна в бывшей «проходной» части у кухни; вход через тамбур 900 из существующего проёма О8. Детская 11,97 закрыта перегородкой с дверью. Постирочная — колонна СМ+СУ, хозяйка, гостевой WC, высокий шкаф (дверь перенесена и сужена до 700). Шкаф прихожей — 3020×600 во всю стену напротив входа.

Плюсы: основной санузел с запасом: проходы 650–840, раковина-тумба 800, шкаф, дверь из зоны у прихожей; гардеробная 4,2 м² (≈ 5 п.м. хранения) + спальная зона 13,0 м² с двумя окнами, вход через тамбур — спальня изолирована от кухни и коридора; изголовье кровати — к новой перегородке гардеробной (буфер от кухни), рабочее место у окна О2; постирочная полностью: колонна, хозяйка, гостевой WC, высокий шкаф; шкаф прихожей 3020 — на всю стену напротив входа; несущие W7/W8/C1 не затрагиваются (только закладка О9 и дверь в О8)

Минусы: расширение мокрой зоны за счёт коридора (над нежилым техподпольем) — гидроизоляция и включение в проект перепланировки; коридор сужается 1300 -> 1000 (норма ≥ 850 выполнена); больше перегородок (5 участков ПГП + закладки) — дороже А на ≈ 150-250 тыс. Р [оценка]; участок водяного ТП коридора (полоса 290 мм) оказывается под полом ванной — не трогаем, электро-ТП над ним не укладываем

Вариант С — «Большая детская»: спальня в 11,97, детская в 17,79 — М 1:100



Комнаты меняются: ребёнку — 17,5 м² с двумя окнами (игровая 2×2, ДСК, место на школьный возраст), родителям — 11,9 м² в тихой части квартиры со шкафом 1960×600 и рабочим местом. Санузел расширяется как в В. Постирочная — без унитаза (максимум хранения, выпуск Ø110 заглушен с доступом).

Плюсы: ребёнку — самая большая комната с двумя окнами: игровая 2×2, ДСК, место под школьный стол и вторую кровать для гостя; родители — в тихой части квартиры, далеко от кухни-кинозоны; комфортный санузел (как в В); постирочная без унитаза — свободнее, больше хранения

Минусы: шкаф родителей 1960 п.м. < программы (2400 п.м. / 1,5 м²) — нужен комод; изголовье родительской кровати — к стене ванной со стояками (шум); рабочее место родителя не у окна (у W6), в 670 мм от кровати; детская смежна с кухней-кинозоной (вечерний шум); нет гостевого WC — утренняя нагрузка на один унитаз (противоречит сценарию «Утро»); расширение мокрой зоны за счёт коридора — как в В

						КВ108-ДП-АР-03			
						Квартира №108, СПб, дизайн-проект			
Изм.	Кол.уч	Лист	№док.	Подп.	Дата	Архитектурные решения	Стадия	Лист	Листов
Разраб.		rib-агенты			10.2026		Р	7	51
Пров.									
ГИП						Варианты планировки А, В, С (рассмотренные) Масштаб 1:100	ПИБ агенты rib-*		
Н.контр.									
Утв.									