


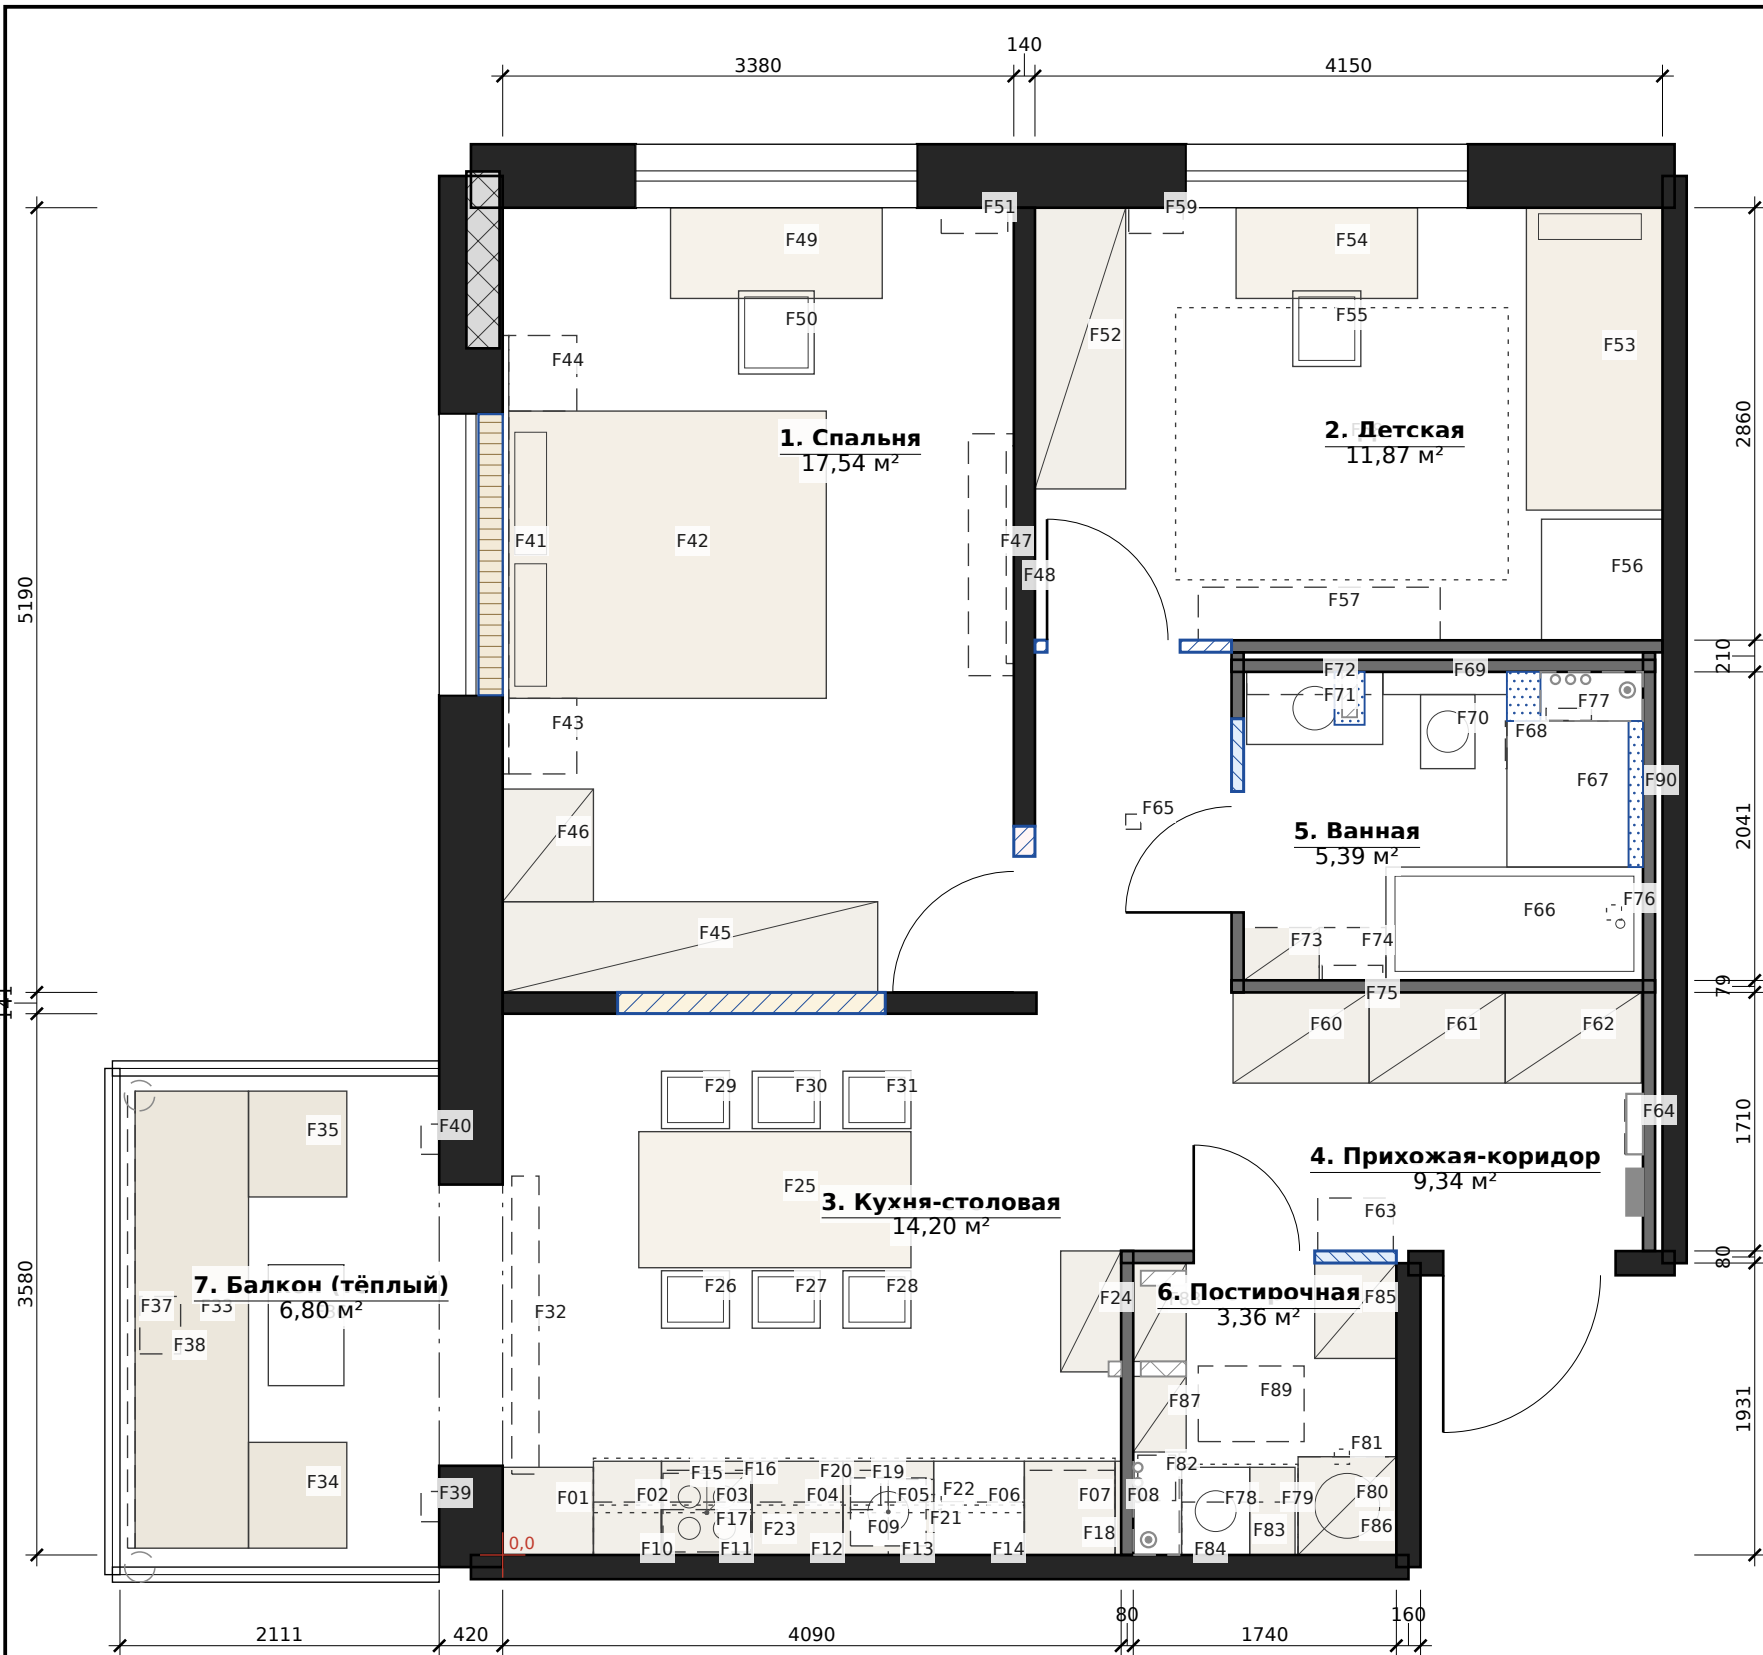

Экспликация мебели и оборудования (furniture.json)

Марка	Пом.	Наименование	ШхГхВ	Положение (от 0,0), мм	Изг.
F01	R3	K-01 Пенал угловой 600 (сухие продукты; ниша встраиваемой СВЧ — опция)	600×580×2400	х 0.600; у 0.580	да
F02	R3	K-02 База 450, 3 ящика (кастроли); в ней розетка духовки	450×620×880	х 600.1050; у 0.620	да
F03	R3	K-03 База 600 под духовой шкаф + индукционная панель	600×620×880	х 1050.1650; у 0.620	да
F04	R3	K-04 База 600, 3 ящика (приборы, основная рабочая зона)	600×620×880	х 1650.2250; у 0.620	да
F05	R3	K-05 База 600 под мойку (влагостойкая ЛДСП, поддон)	600×620×880	х 2250.2850; у 0.620	да
F06	R3	K-06 ПММ полновстраиваемая 600 (14 комплектов), 2,0 кВт	600×620×820	х 2850.3450; у 0.620	
F07	R3	K-07 Пенал 600 под встраиваемый холодильник (ниша 1780-1940)	600×620×2400	х 3450.4050; у 0.620	да
F08	R3	K-08 Доборная панель 40 у W10	40×620×2400	х 4050.4090; у 0.620	да
F09	R3	Столешница кварцевый агломерат 20 мм, 3450×640 (в 600..4050), вырезы: мойка, индукция	3450×640×20	х 600.4050; у 0.640; низ +880	да
F10	R3	KW-01 Навесной 450	450×350×850	х 600.1050; у 0.350; низ +1550	да
F11	R3	KW-02 Навесной 600 со встроенной вытяжкой	600×350×850	х 1050.1650; у 0.350; низ +1550	да
F12	R3	KW-03 Навесной 600	600×350×850	х 1650.2250; у 0.350; низ +1550	да
F13	R3	KW-04 Навесной 600 с сушикой над мойкой	600×350×850	х 2250.2850; у 0.350; низ +1550	да
F14	R3	KW-05 Навесной 600	600×350×850	х 2850.3450; у 0.350; низ +1550	да
F15	R3	Индукционная варочная панель 60 см, 4 зоны, 7,4 кВт	580×520×60	х 1060.1640; у 20.540; низ +840	
F16	R3	Духовой шкаф встраиваемый 60 см, 3,5 кВт	600×560×595	х 1050.1650; у 0.560; низ +160	
F17	R3	Вытяжка встраиваемая 60 см в KW-02, 250-600 м³/ч, обратный клапан	600×300×300	х 1050.1650; у 0.300; низ +1550	
F18	R3	Холодильник встраиваемый 1780-1940 (в K-07), 0,2 кВт	600×560×1900	х 3450.4050; у 0.560; низ +160	
F19	R3	Мойка кварцевая 1 чаша 500×450 + смеситель с краном питьевой воды	500×450×200	х 2300.2800; у 60.510; низ +700	
F20	R3	Фильтр питьевой 3-ступенчатый под мойкой (без накопителя)	200×260×400	х 2300.2500; у 300.560; низ +160	
F21	R3	Сортировка мусора выдвижная в K-05	300×500×400	х 2550.2850; у 0.500; низ +160	
F22	R3	Датчик протечки под мойкой/ПММ (на полу за цоколем)	100×100×20	х 2800.2900; у 300.400	
F23	R3	Подсветка рабочей зоны LED 2700K CRI≥90 под навесными KW-01..05	2850×50×10	х 600.3450; у 280.330; низ +1540	
F24	R3	Буфет 400×800 h 2100 вдоль W10 (низ — шкаф, ниша +900..+1400 под чайники/капсульную кофемашину, верх — стекло)	800×400×2100	х 3690.4090; у 1211.2011	да
F25	R3	Стол обеденный 1800×900 (6 перс.)	1800×900×760	х 900.2700; у 1900.2800	
F26	R3	Стул мягкий	450×380×900	х 1050.1500; у 1500.1880	
F27	R3	Стул мягкий	450×380×900	х 1650.2100; у 1500.1880	
F28	R3	Стул мягкий	450×380×900	х 2250.2700; у 1500.1880	
F29	R3	Стул мягкий	450×380×900	х 1050.1500; у 2820.3200	
F30	R3	Стул мягкий	450×380×900	х 1650.2100; у 2820.3200	
F31	R3	Стул мягкий	450×380×900	х 2250.2700; у 2820.3200	
F32	R3	Экран моторизованный 80" 16:9 tab-tension (полотно 1771×996), корпус в нише ламбрекена у О4	1971×180×150	х 60.240; у 535.2506; низ +2550	
F33	R7	П-диван: спинная секция вдоль остекления B1, 750×3023 (на ножках)	3023×750×850	х -2431..-1681; у 45.3068	да
F34	R7	П-диван: боковая секция у B3, 650×700	650×700×850	х -1681..-1031; у 45.745	да
F35	R7	П-диван: боковая секция у B2, 650×700, с вентилируемым отсеком AV (ресивер/медиателер)	650×700×850	х -1681..-1031; у 2368.3068	да
F36	R7	Пуф-стол 500×800	500×800×400	х -1550..-1050; у 1120.1920	
F37	R7	Ближкнут-портьеры на потолочном П-образном карнизе с электроприводом (B1+B2+B3)	50×3023×2400	х -2481..-2431; у 45.3068; низ +100	
F38	R7	Проектор 4K, throw ratio с зумом, вкл. 1.29; lens shift; ≤ 28 дБ — на потолке балкона	380×270×130	х -2400..-2130; у 1330.1710; низ +2250	
F39	R7	Колонка настенная R (правая для зрителя) на простенке W2 со стороны балкона	200×120×300	х -540..-420; у 220.420; низ +1050	
F40	R7	Колонка настенная L на простенке W2 со стороны балкона	200×120×300	х -540..-420; у 2650.2850; низ +1050	
F41	R1	Буазери стены-изголовья W2 (M06), центральная филёнка 1860 над зашитым O1 — съёмная	40×2900×2700	х 0.40; у 5166.8066	да
F42	R1	Кровать 1800×2000 (рама =1900×2100) с мягким изголовьем, на глайдерах	1900×2100×1150	х 40.2140; у 5666.7566	
F43	R1	Тумба прикроватная подвесная 450×500 (сторона входа)	500×450×350	х 40.490; у 5166.5666; низ +300	
F44	R1	Тумба прикроватная подвесная 450×500 (сторона окна)	500×450×350	х 40.490; у 7566.8066; низ +300	
F45	R1	Шкаф-купе Г — длинная часть 2480×600 до потолка вдоль NW1/W8 (M07)	2480×600×2700	х 0.2480; у 3721.4321	да
F46	R1	Шкаф Г — короткая часть 745×600 вдоль W2 (распашная дверь 745 — купе на 745 не работает)	745×600×2700	х 0.600; у 4321.5066	да
F47	R1	ТВ-консоль подвесная 1600×300 (низ +250 под робот-пылесос)	1600×300×200	х 3080.3380; у 5816.7416; низ +250	да
F48	R1	ТВ 65" на плоском кронштейне (центр +1150, ось у=6616)	1440×50×810	х 3330.3380; у 5896.7336; низ +745	
F49	R1	Стол рабочий 1400×600 у окна O2 (столешница дуб, подстолье/консоль на стене)	1400×600×750	х 1110.2510; у 8311.8911	да
F50	R1	Кресло рабочее	500×550×1000	х 1560.2060; у 7811.8361	
F51	R1	Бризер (класс Тип 45 / Ballu Oneair) в простенке справа от O2	440×170×520	х 2900.3340; у 8741.8911; низ +1700	
F52	R2	Шкаф детский 600×1800 h 2400 (2 секции по 900, распашной)	1860×600×2400	х 3520.4120; у 7051.8911	да
F53	R2	Кровать 900×2000 с ящиками для игрушек	900×2000×450	х 6770.7670; у 6911.8911	
F54	R2	Стол «растущий» 1200×600 у окна O3 (по оси окна)	1200×600×750	х 4850.6050; у 8311.8911	
F55	R2	Стул «растущий»	450×500×800	х 5225.5675; у 7861.8361	
F56	R2	ДСК настенный 800×800 (к W6 и потолку, без опоры в пол)	800×800×2500	х 6870.7670; у 6051.6851	
F57	R2	Стеллаж низкий навесной 1600×350 h 600 (игрушки, на уровне ребёнка)	1600×350×600	х 4600.6200; у 6051.6401; низ +100	да
F58	R2	Игровая зона 2200×1800 (ковёр)	2200×1800×10	х 4450.6650; у 6450.8250	
F59	R2	Бризер компактный (ширина ≤ 360) в простенке между шкафом и O3	360×170×500	х 4140.4500; у 8741.8911; низ +1800	
F60	R4	Шкаф прихожей, секция 1 — 900 (2 двери 450); ниша робота-пылесоса внизу h 400 без фасада, хоз. хранение	900×600×2650	х 4830.5730; у 3121.3721	да
F61	R4	Шкаф прихожей, секция 2 — 900 (2 двери 450); верхняя одежда, штанга + антресоль	900×600×2650	х 5730.6630; у 3121.3721	да
F62	R4	Шкаф прихожей, секция 3 — 900 (дверь-зеркало в рост 450 + дверь 450); отсек самоката/коляски h 1400, обувь, антресоль	900×600×2650	х 6630.7530; у 3121.3721	да
F63	R4	Банкетка откидная 500×350 на NW9 (в сложенном виде 100)	500×350×450	х 5390.5890; у 2011.2361	да
F64	R4	СС-щит U16: роутер, шлюз умного дома (Zigbee), контроллер защиты от протечек	х 7421.7541; у 2650.3050; низ +1550		
F65	R4	Точка доступа Wi-Fi потолочная (PoE) в коридоре, на потолке +2650 (D19)	100×100×40	х 4120.4220; у 4800.4900; низ +2610	
F66	R5	Ванна 1700×750 акрил/кварил на ножках, экран с ревизией сифона	1700×750×600	х 5841.7541; у 3800.4550	
F67	R5	Душ walk-in 805×966 в свету (после облицовки W14 VK-C1), линейный трап вдоль облицовки, душевая система скрытого монтажа	805×966×0	х 6641.7446; у 4550.5516	
F90	R5	Облицовка W14 в душе VK-C1 (~95); ниши 500×400 (+1200..+1600) и 500×250 (+600..+850) от пола ванной, ось у 5150, глубиной ≤ 70; корпус термостата у 4750, h 1100 (D23, clashes F-04); трасса сифона ванны ...	95×966×2450	х 7446.7541; у 4550.5516	да
F68	R5	Стекло душа фиксированное 315, 8 мм (к стене + стабилизатор к потолку, профиль пола на клею)	10×315×2000	х 6631.6641; у 5201.5516	
F69	R5	Инсталляция WC (рама только к стене) + короб ГКЛВ 150 до +1200 с полкой	821×150×1200	х 5820.6641; у 5691.5841	да
F70	R5	Унитаз подвесной безободковый (ось х 6250)	360×490×400	х 6070.6430; у 5201.5691	
F71	R5	Тумба подвесная 900×480 (2 ящика), столешница + раковина смещена влево	900×480×380	х 4920.5820; у 5361.5841; низ +500	да
F72	R5	Зеркальный шкаф 900×750×150 с LED и розеткой	900×150×750	х 4920.5820; у 5691.5841; низ +1150	да
F73	R5	Пенал подвесной 500×350 до +2200	500×350×2000	х 4900.5400; у 3800.4150; низ +200	да
F74	R5	Тумба-корзина для белья 440×350 h 700 (подвесная)	441×350×700	х 5400.5841; у 3800.4150; низ +150	да
F75	R5	Полотенцесушитель электрический 400×800 над корзиной (класс II, IP44)	400×100×800	х 5420.5820; у 3800.3900; низ +950	
F76	R5	Датчики протечки ванной х3: под ванной у сифона справа (ревизия H6), под тумбой у U14, у короба U10 / трапа	100×100×20	х 7300.7400; у 4200.4300	

Экспликация мебели и оборудования (furniture.json) (продолжение)

Марка	Пом.	Наименование	ШхГхВ	Положение (от 0,0), мм	Изг.
F77	R5	Электрокраны ХВС/ГВС узла N1 в коробе U10 (зона люка H1 +500..+1100)	300×80×100	х 6900..7200; у 5520.5600; низ +650	
F78	R6	Тумба хозяйки 450 (влагостойкая ЛДСП) + мойка накладная 450	450×580×880	х 4490..4940; у 0.580	да
F79	R6	Карго 300 (бытовая химия)	300×580×880	х 4940..5240; у 0.580	да
F80	R6	Колонна СМА (низ) + сушильная машина с тепловым насосом (верх), монтажный комплект; ниша 650×650	650×650×1750	х 5260..5910; у 0.650	
F81	R6	Датчики протечки х3: под колонной, под хозяйкой, у коллектора U11	100×100×20	х 5500.5600; у 600.700	
F82	R6	Электрокраны ХВС/ГВС узла N2 в коробе U5 (зона люка H3 +950..+1350)	250×300×100	х 4200..4450; у 360.660; низ +1000	
F83	R6	Столешница компакт-плита 12 мм над хозяйкой и карго 770×600	770×600×12	х 4490..5260; у 0.600; низ +880	да
F84	R6	Навесные шкафы 350 над столешницей, до потолка (+1450..+2500)	770×350×1050	х 4490..5260; у 0.350; низ +1450	да
F85	R6	Пенал ЛДСП 540×630 до потолка +2500 (гладильная доска, вертикальный пылесос, швабра, стремянка)	540×630×2500	х 5370..5910; у 1300.1930	да
F86	R6	Антресоль над колонной 650×650, +1800..+2500	650×650×700	х 5260..5910; у 0.650; низ +1800	да
F87	R6	Шкаф ЛДСП 350 у W10 между коробом U5 и вентканалом U12 (500), до потолка +2500	500×350×2500	х 4170..4520; у 681.1181	да
F88	R6	Шкаф ЛДСП 350 у W10 над коллектором U11 (650); нижний ярус 450 — фасады от пола без дна, выше полки	650×350×2500	х 4170..4520; у 1280.1930	да
F89	R6	Сушилка потолочная «лиана» 4 прутка (ручная)	700×500×100	х 4600..5300; у 750.1250; низ +2300	

Общие указания

- Водяной ТП в стяжке (D3); ни одно изделие не крепится к полу. Корпусная мебель — на регулируемых опорах + крепление к стенам от опрокидывания; навесная — к стенам; ДСК, стекло душа, инсталляция — к стенам/потолку; купе — верхнеподвесная система (нижний рельс только на клею); ограничители дверей — настенные.
- Встроенная мебель над водяным ТП — цоколь с вентрешёткой/зазором ≥ 20 мм сверху и снизу (не загипать тепло, перегрев покрытия). Электро-ТП (су, балкон) под мебелью без ножек и под ванной/колонной СМА не укладывается.
- Коллекторы ТП U11, U14 (h 400) — только под мебелью с открытым доступом (съёмный цоколь / фасады от пола без дна).
- Вентканалы U12/U13, U25, U26 не перекрываются: буфет кухни ≤ 2100 под решёткой U13; шкафы постирочной — по обе стороны U12; люки коробов U5/U10 свободны.
- Все размеры встроенной мебели — уточнить по месту после выравнивания стен (questions №1).

КВ108-ДП-АР-07

Квартира №108, СПб, дизайн-проект

Изм.	Кол.уч	Лист	№док.	Подп.	Дата	Архитектурные решения	Стадия	Лист	Листов
Разраб.		rib-агенты			10.2026		Р	11	51
Пров.						План расстановки мебели и оборудования Масштаб 1:50	ПИБ агенты rib-*		
ГИП									
Н.контр.									
Утв.									