


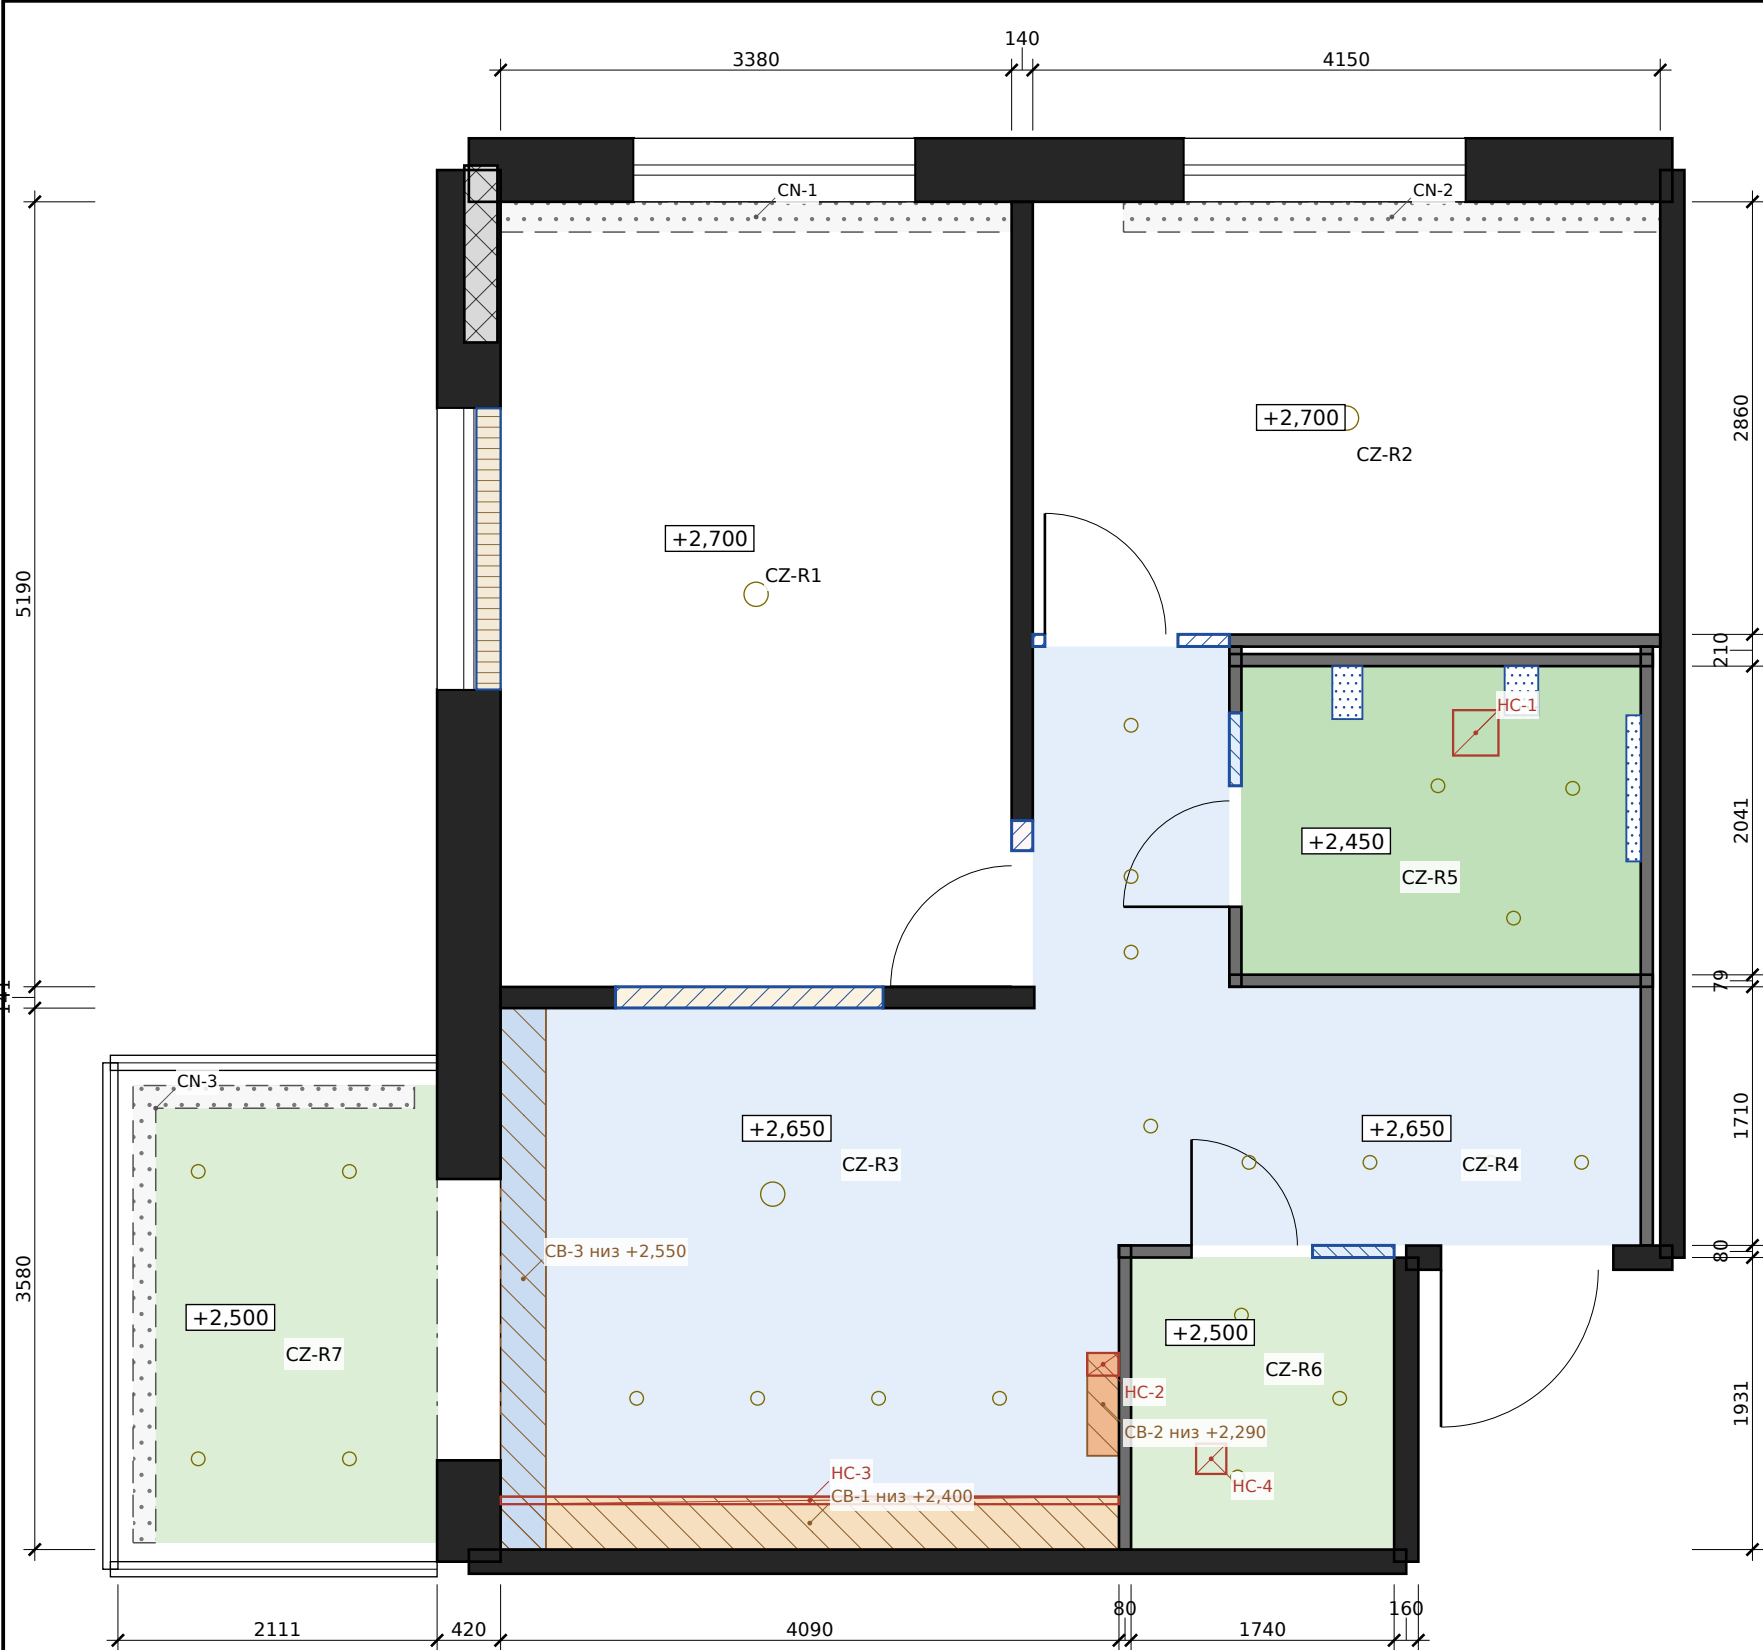

Условные обозначения

- Потолок +2,700
- Потолок +2,650
- Потолок +2,500
- Потолок +2,450
- Короб/опуск ГКЛ (низ — по подписи)
- Ниша под карниз штор
- Люк / ревизия в потолке
- Встроенный светильник (по ЭО-01)

Типы потолков

Зона	Пом.	Отметка	Конструкция	Отделка
CZ-R1	R1	+2,700	ГКЛ (ГСП-А) 12,5 по каркасу ПП 60/27 на прямых подвесах, пленум 50 до плиты (гофра ≤ Ø20, D15)	шпаклёвка Q4, глубококоматовая краска C1 (класс 2)
CZ-R2	R2	+2,700	ГКЛ (ГСП-А) 12,5 по каркасу ПП 60/27 на прямых подвесах, пленум 50	шпаклёвка Q4, глубококоматовая краска C1
CZ-R3	R3	+2,650	ГКЛ (ГСП-А) 12,5 по каркасу ПП 60/27 на подвесах, пленум 100 — ЛОКАЛЬНОЕ Понижение всей кухни под группу встроенных спотов L2 (глубина ≤ 80)	шпаклёвка Q4, глубококоматовая краска C1
CZ-R4	R4	+2,650	ГКЛ (ГСП-А) 12,5 по каркасу ПП 60/27 на подвесах, пленум 100 — магистраль кабелей от щита U15 (D15) и встроенные споты L15/L16	шпаклёвка Q4, глубококоматовая краска C1
CZ-R5	R5	+2,450	ГКЛВ 12,5 по каркасу ПП 60/27 на подвесах (оцинк.), пленум 300: вентилятор EF1, Ø100 к U26, кабели	влагостойкая краска C1 (класс 1, для влажных помещений); по стенам с плиткой до потолка — теневой шов 10×10 (профиль), над окрашенными стенами — карниз h 40 (M22, вне душа)
CZ-R6	R6	+2,500	ГКЛВ 12,5 по каркасу ПП 60/27 на подвесах, пленум 250: вентилятор EF2, Ø100 к U25 (K-08)	влагостойкая краска C1
CZ-R7	R7	+2,500	ГКЛВ 12,5 по каркасу на подвесах под утеплителем PIR 50 (к плите вышележащего балкона), пленум ≈ 150-200 [ДОПУЩЕНИЕ №51]	краска C6 тёмная олива глубококоматовая (≤ 3 gloss)

Короба, ниши штор, люки

Марка	Низ / размер	Описание
CB-1	+2,400	Карниз-короб над навесными (воздуховод КН1 Ø125, розетки P-K10/P-K10a)
CB-2	+2,290	Короб-опуск вентиляции вдоль W10 (КН1 к решётке U13) — clashes K-12
CB-3	+2,550	Короб-ламбрекен портала O4 с нишей экрана 80"
CN-1	200	потолочный профильный карниз ≤ 35 мм, 2 ряда (блэкаут + тюль), x 700..2800 (бризер F51 x ≥ 2900 — не закрывается, D-M09 отступ ≥ 100)
CN-2	200	профильный карниз ≤ 35 мм, 2 ряда, x 4520..6700 (бризер F59 x 4140..4500 — свободен)
CN-3	150	П-образный моторизованный карниз F37 (привод у угла B1/B3, P-B02), блэкаут; трек в 110 от стекла — между портьерой и стеклом зазор для приточных клапанов SV1/SV2 (K-13)
HC-1	300×300	люк-невидимка под покраску, влагостойкий, с уплотнителем; воздуховод EF1 → U26, распаечная коробка L19/P-V05
HC-2	210×150	съёмная вентрешётка в низе короба CB-2; обратный клапан Ø125 у решётки U13, естественная вытяжка кухни
HC-3	фронт CB-1	съёмная MDF-панель карниза; розетки P-K10/P-K10a, БП подсветки, соединения КН1
HC-4	Ø200 (корпус EF2)	съёмный корпус вентилятора EF2; воздуховод Ø100 0,4 м к U25 (врезка +2550..2700 в грань U5)

Указания

- 1. По умолчанию чистовой потолок +2700, зазор 50 под кабели в гофре (D15) — спальня и детская: встроенных спотов нет, свет — люстры, бра, LED в карнизах (сопсерт п.5).
 - 2. Там, где группы встроенных спотов (кухня L2, прихожая L15, коридор L16) — ЛОКАЛЬНОЕ Понижение помещениями: кухня + прихожая + коридор одной плоскостью +2650 (пленум 100 — ГКЛ 12,5 = 87,5 ≥ 80); без перепадов на открытой границе кухня/прихожая (D19).
 - 3. Понижение коридора +2450..2500 из концепции/doors.json отменено: воздуховодов в коридоре нет (hvac.json), кабельной магистрали хватает пленума 100 (D19).
 - 4. Мокрые помещения — ГКЛВ по ОВ: ванная +2450 (EF1), постирочная +2500 (EF2, K-08), балкон +2500 (утеплитель, проектор).
 - 5. Все светильники и подвесы тяжелее 3 кг (люстры, проектор, сушилка, ДСК, карниз штор с приводом) — к плите через закладные/дистанционные втулки, не к ГКЛ.
 - 6. Карнизы — полиуретан гладкий (M04), тон C1; в спальне по W2 — карниз буазери с теневым пазом LED; в мокрых зонах с плиткой до потолка — теневой профиль 10 мм вместо карниза.
 - 7. Натяжные и реечные потолки не применяются (сопсерт/M03: ровный окрашенный потолок неоклассики).
- отметки от УЧП ±0.000 (верх плиты +100); низ плиты перекрытия +2750; в ванной высота от пола ванной = отметка – 80

						КВ108-ДП-АР-09			
						Квартира №108, СПб, дизайн-проект			
Изм.	Кол.уч	Лист	№док.	Подп.	Дата	Архитектурные решения	Стадия	Лист	Листов
Разраб.		rib-агенты			10.2026		Р	13	51
Пров.									
ГИП									
Н.контр.						План потолков Масштаб 1:50	ПИБ агенты rib-*		
Утв.									