


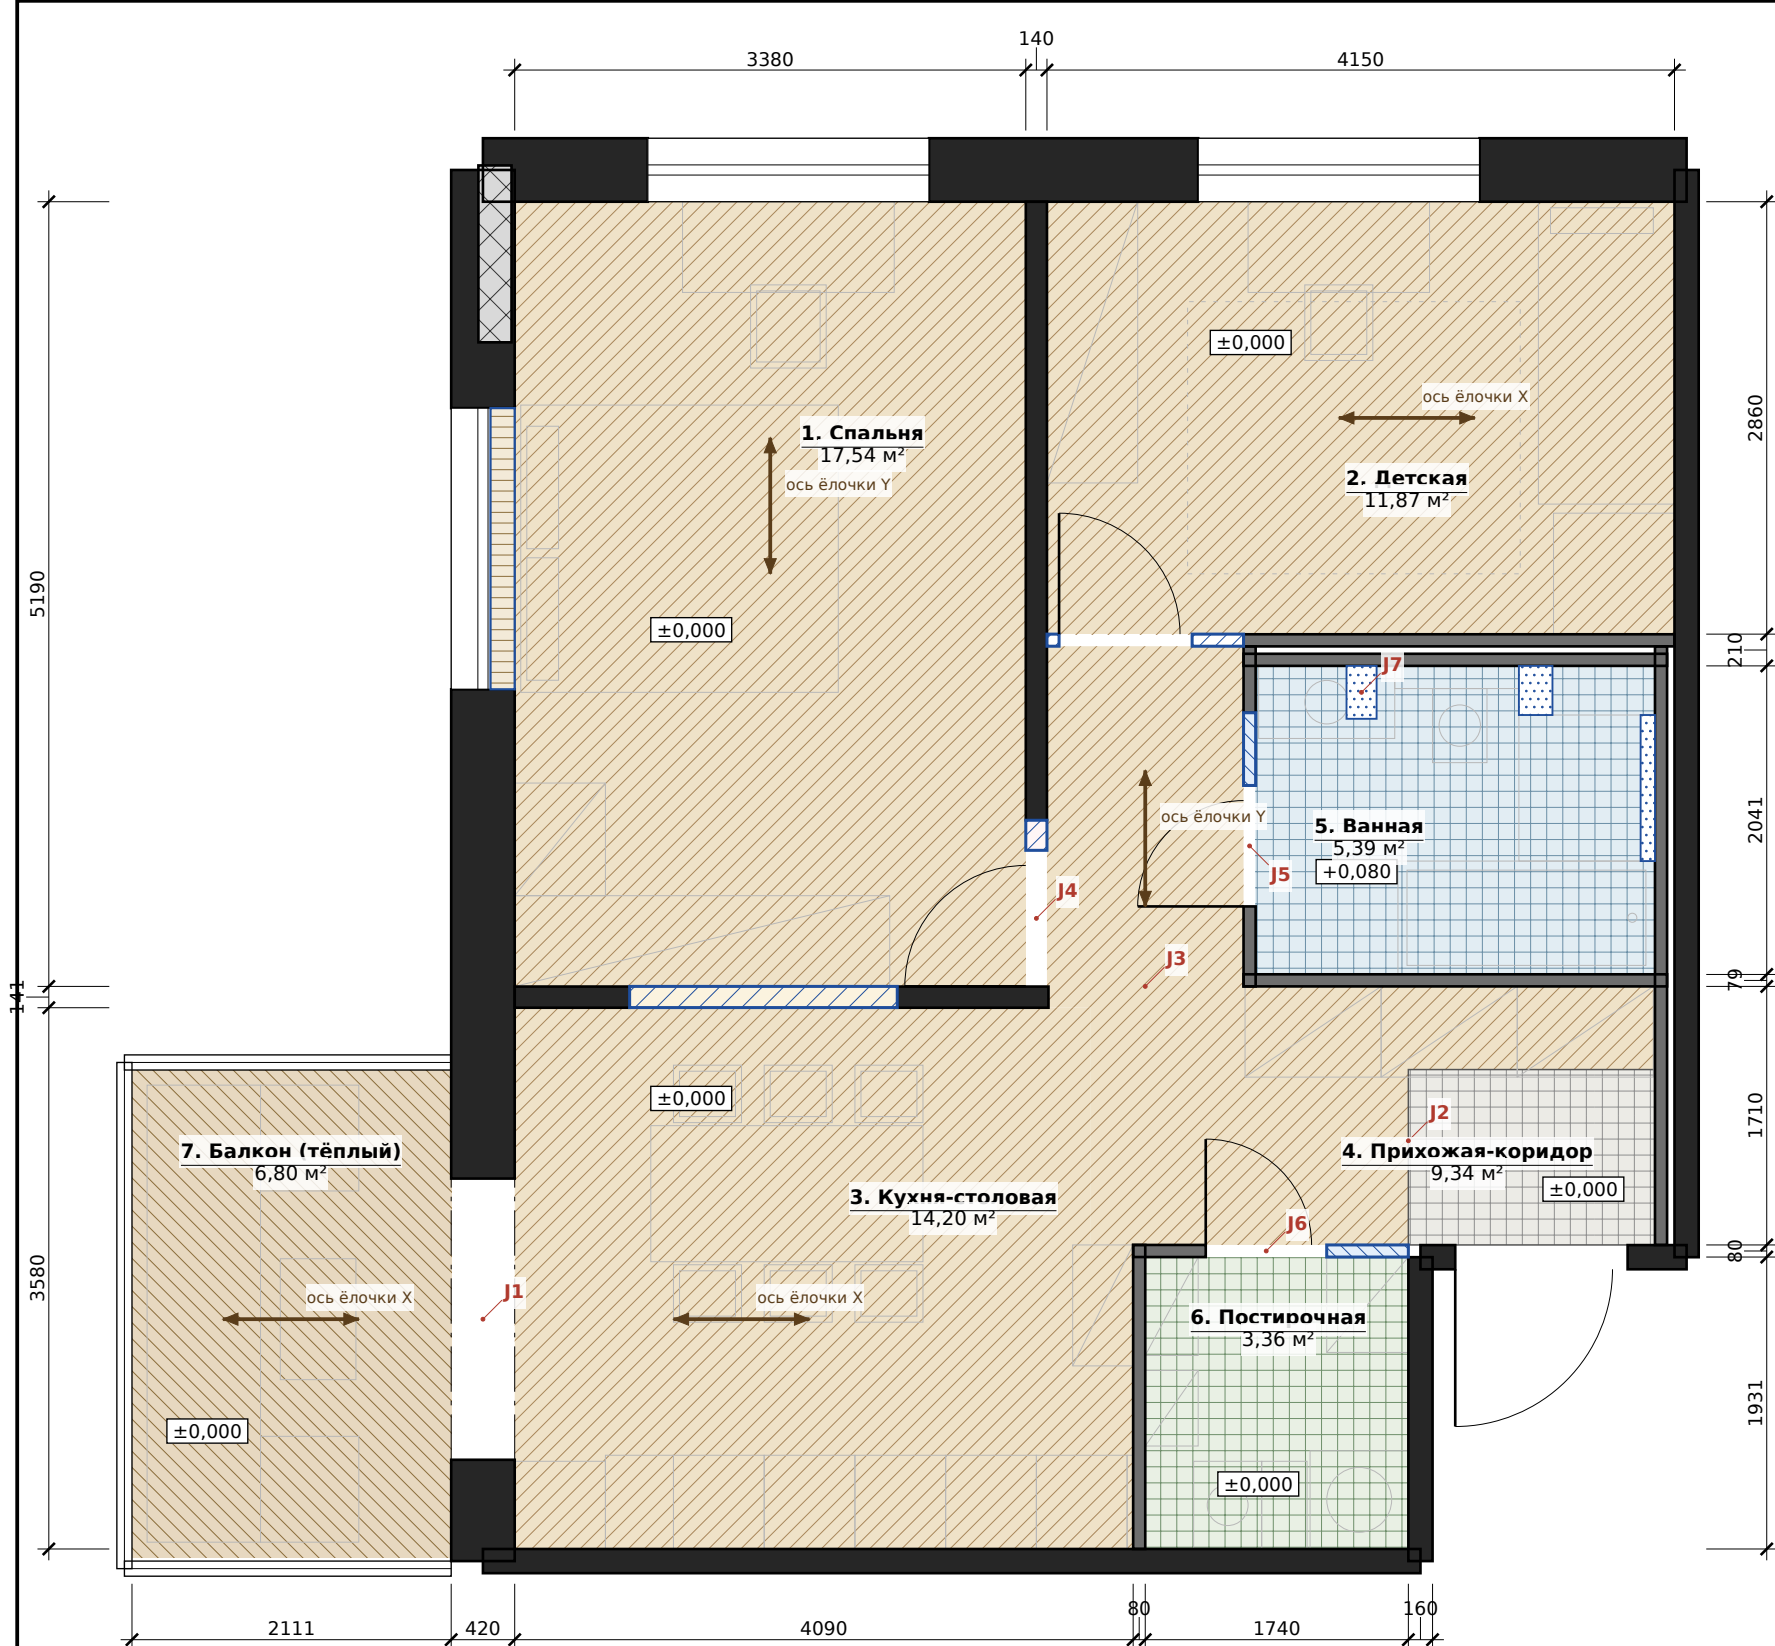

Условные обозначения

	M01 инж. доска дуб «ёлочка» (P-OAK)
	M16 керамогранит 600×600 у входа (P-TILE-HALL)
	M20 керамогранит, подиум +80 (P-BATH)
	M25 керамогранит 600×600 (P-LAUNDRY)
	M28 LVT «ёлочка» (P-BALC)
	Стык покрытий / порог (таблица ниже, узлы AP-17/18)

Ведомость покрытий

Пом.	Покр.ти	Пирог	Отм.	Обогрев	Плнтус
R1	M01 инж. доска дуб ёлочка	P-OAK	±0,000	водяной (сущ.)	M02 МДБ h 120 С2, только к стене
R2	M01 елочка	P-OAK	±0,000	водяной (сущ.)	M02 h 120 С5
R3	M01 елочка	P-OAK	±0,000	водяной (сущ.)	M02 С2; за кухней — цоколь мебели
R4	M01 елочка + M16 керамогранит у входа	P-OAK / P-TILE-HALL	±0,000	водяной (сущ.)	M02 С2-у керамогранита — плитус из керамогранита h 10...
R5	M20 керамогранит 60×60 / 60×120 R10 (в/в г/у/в)	P-BATH	+0,080	электро TP1 1,89 м ² (electric/iso), не под ванной/душеш/коробами/U14	нет — плитка до пола, керамик
R6	M25 керамогранит 60×60 R10	P-LAUNDRY	±0,000	электро TP2 1,06 м ² , не под колонн/шкафами/U11	плитка/кромка шкафов
R7	M28 LVT клеевой ёлочка	P-BALC	±0,000	электро TP3 2,32 м ² (сводбный пол), t ≤ +27 °C	МДФ наложки h 80 С6 по паркетам /Пдвиган в остоян

Пироги полов (floors.json)

Пор	Слой (снизу вверх)	мм / отм.
P-ОАК	Инженерная доска дуб ёлочка на клею (M01) по стяжке с водным ТП	верх 0
	плита перекрытия (верх)	-100
	стяжка с водным ТП застройщика (существующая, не трогать)	80
	грунт + локальный ремонтный состав (до 3)	3
	клей МS-полимер эластичный (зубчатый шпатель 811)	2
	инженерная доска 2-слойная 15 (90х600, ёлочка 1:6)	15
P-TILE-HALL	Керамогранит 60х60 R10 у входа (M16)	верх 0
	плита	-100
	стяжка с водным ТП (сущ.)	80
	грунт, ремонтный состав	2
	клей C2TE S1 (эластичный, для ТП)	8
	керамогранит 600х600х10 ректифицикат	10
P-LAUNDRY	Керамогранит 60х60 R10 + электро-ТП TP2 (M25)	верх 0
	плита	-100
	стяжка с водным ТП (сущ.)	80
	обмазочная гидроизоляция 2 слоя + ленты в углах, заход на стены 200	2
	клей C2TE S1 с нагревательным матом TP2 (мат 3 в слое клея)	8
	керамогранит 600х600х10	10
P-BATH	Подиум ванной +80 (D18), керамогранит + электро-ТП TP1 (M20)	верх 80
	плита	-100
	стяжка с водным ТП (сущ.), верх — 20 — не резать (D3/D4)	80
	грунт + нижняя обмазочная гидроизоляция (барьер над ТП и техноподемьем), заход 200 над чистым полом	1.5
	демфенированная лента 10 по периметру; трубы Ø50 трапа/ванны — на стяжке, защитный слой ≥ 30	0
	подиум ЦПС M300 фиброармированная + сетка 50х50 Вр4; в душе уклон 1.5 % к трапу	78.5
	основная обмазочная гидроизоляция 2 слоя, ленты, мажнжета/флэши трапа, вклеяка в ранку U14	2
	клей C2TE S1 + мат TP1 (вне ванны, душа, коробо: ≥ 100 от рамки U14)	8
P-BALC	Пол балкона до ±0.000 (D1, D17, D22): утепление + стяжка + электро-ТП TP3 + LVT (M28)	верх 0
	плита балкона [ДОПУЩЕНИЕ N46]	-120
	грунт, ремонт плиты, выравнивание перепадов > 5	0
	XPS 300 кПа 50 (швы проклеены), по периметру — XPS 20 на паралет	50
	пленка ПБ 200 мкм (пароизоляция), нахлест 100, завод на стены 100) + демпфирующая лента 10	0
	стяжка ЦПС M300 фибра + сетка Вр4 50х50 (плавающая)	55
	нагревательный мат TP3 (только свободный пол) в самовыравнивающей смеси, ≥ 5 над матом	10
	грунт + клей для LVT (дисперсионный, допуск ТП)	0.5
	LVT клеевой ёлочка 4.5 (слои износа ≥ 0.55)	4.5

Стыки и пороги

Стык	Где	Детали
J1	кухне/балкон, портал О4: х=—210 (осы стены), у=590.2450	Узел 1 (details.mtd): заголовок, пробковый компенсатор 5 + лутунг Д-профиль 8 на клею (без саморезов в пол)
J2	прихожая: х=5910 (у 2011.317) и у=3171 (х 5910.7541)	О4: заголовок, пробка 5 + лутунговая вставка 3
J3	коридор/прихожая у=3721, х 3520.4820	Физ 2х90 заголовок, без компенсатора
J4	двери D1 (х 3450, у 3721.4621) и D2 (у 6011, х 3600.4480)	шов-компенсатор: 5 пол плоскостной полотна; без порога; подрез полотна 20 (К-14)
J5	авьер D3, W12 х 4820.4900, у 4250.5050	Узел 5: порог-ступень из керамогранита SX (массив/ступень 20 мм ополный UH3), авер +90 = пол планок +10 (ограничитель вду); ступень 90 из коридора с контрастной доской; гидроизоляция заведена на порог + пол коридору; лавду: Не делается (уключ к двери вывел бы воду в коридор) — D20
J6	авьер D4, W11 х 4570.5370	порог-ограничитель керамогранит/ламель 15 со скругленными краями, на клею; гидроизоляция заведена под порог
J7	рамка U14 в ванной у 5501.5700, у 5491.5841 (VK-3, K-05)	Узел 6: бортик из UCP20/нерж. уголка, авер +100 (на 20 выше пола ванной); гидроизоляция с подиума заведена на бортик и втулку до дна ниши; облицовка бортика плиткой; сдвинутый шовок F71 перед нишей

						КВ108-ДП-АР-10			
						Квартира №108, СПб, дизайн-проект			
Изм.	Кол.уч	Лист	№док.	Подп.	Дата	Архитектурные решения	Стадия	Лист	Листов
Разраб.		rib-агенты			10.2026		Р	14	51
Пров.									
ГИП						План полов Масштаб 1:50	ПИБ агенты rib-*		
Н.контр.									
Утв.									