


Кухня — W3: фронт и фартук

из кухни на юг (–Y): слева х=4090, справа х=0 М 1:25

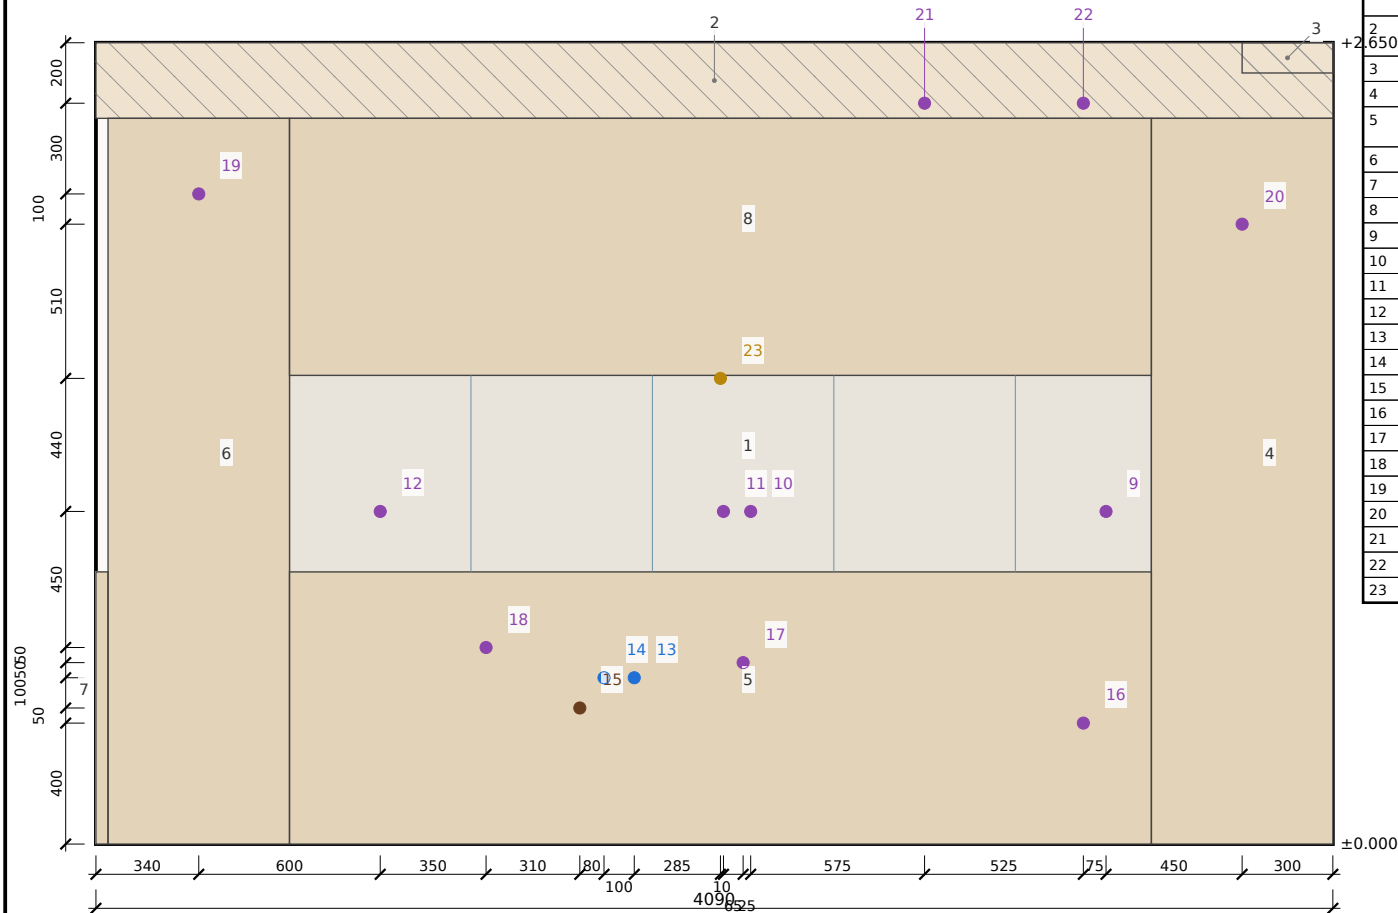


Отделка: стена за мебелью — шпаклёвка Q2 + грунт; фартук M13; карниз-короб СВ-1 — C2

№	Элемент	s, мм	z, мм
1	фартук керамогранит 600×1200 «мрамор» С9 (M13), вертикально, подрезка 650 по высоте	600..3450	900..1550
2	карниз-короб СВ-1 + 2400..+2650 (фронт у=350, съёмная панель)	0..4090	2400..2650
3	ламбрекен СВ-3 (сечение у W2), низ +2550	0..300	2550..2650
4	К-01 пенал 600 h 2400	0..600	0..2400
5	К-02..К-06 базы (цоколь 160, корпус, столешница кварц 20 верх +900)	600..3450	0..900
6	К-07 пенал холодильника 600 h 2400	3450..4050	0..2400
7	К-08 доборная 40	4050..4090	0..900
8	навесные КВ-01..05 +1550..+2400	600..3450	1550..2400
9	Р-К05 фартук	750	1100
10	Р-К07 фартук	1925	1100
11	Р-К08 фартук	2015	1100
12	Р-К06 фартук + S3	3150	1100
13	ХВС мойки ½"	2310	550
14	ГВС мойки ½"	2410	550
15	канализация мойки Ø50	2490	450
16	Р-К02 духовка (за К-02)	825	400
17	Р-К03 индукция 32А	1950	600
18	Р-К04 ПИМ	2800	650
19	Р-К09 холодильник	3750	2150
20	Р-К01 СВЧ (опция)	300	2050
21	Р-К10 вытяжка (в карнизе)	1350	2450
22	Р-К10а БП подсветки (в карнизе)	825	2450
23	L1 подсветка рабочей зоны (под навесными)	2025	1540

Кухня — W2 с порталом О4 и ламбрекеном экрана

из кухни на запад (–X): слева у=3580, справа у=0 М 1:25

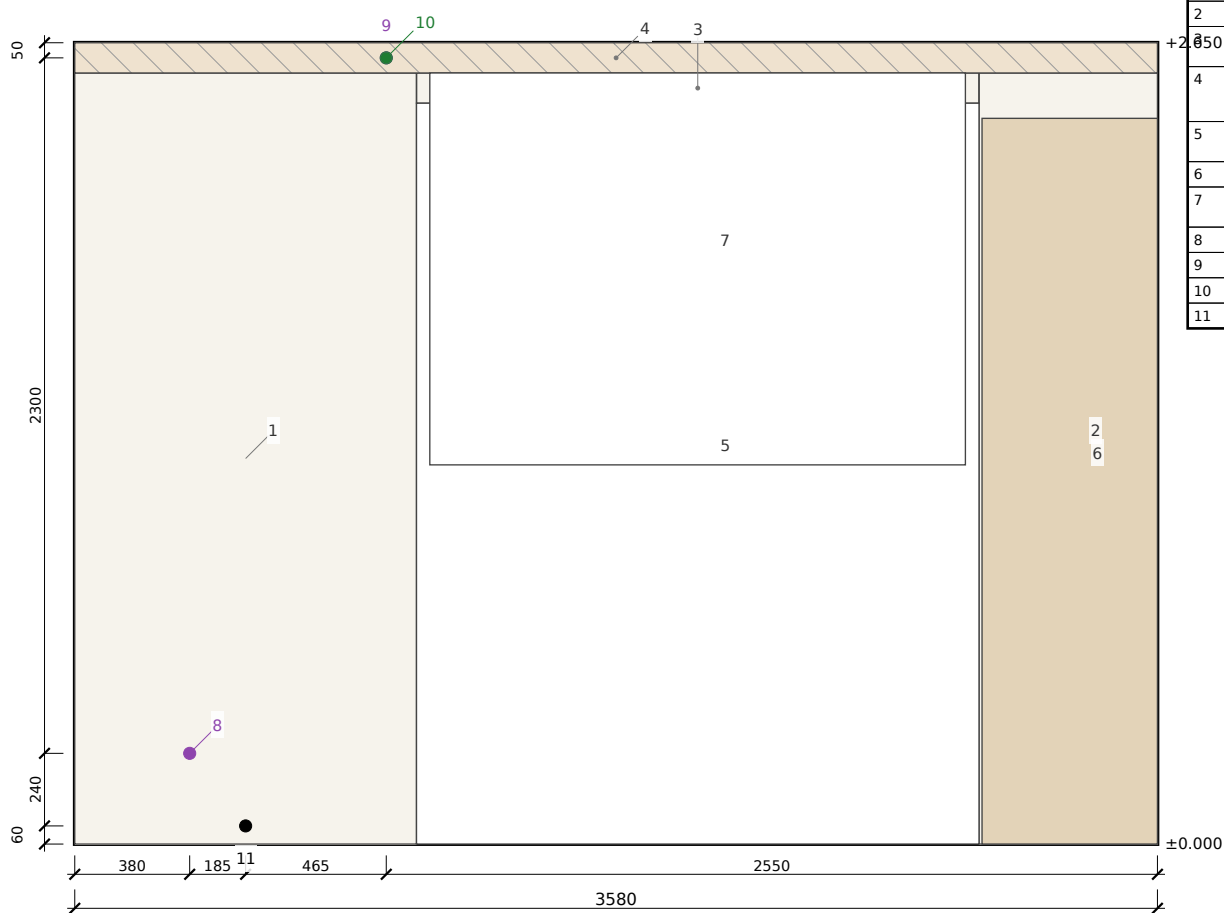


Отделка: Q3 + флизелин + краска C2 класс 1; откосы портала 420 — штукатурка, уголок, C1; ламбрекен C1 / ниша C6

№	Элемент	s, мм	z, мм
1	краска C2 класс 1	2450..3580	0..2550
2	краска C2 (простенок 590 за пеналом — грунт)	0..590	0..2550
3	полоса над перемычкой +2450..+2550 — C1 в цвет откосов (продолжение портала)	590..2450	2450..2550
4	ламбрекен СВ-3 по всей стене, низ +2550, карниз-профиль 60, ниша экрана у 535..2506 (C6 внутри)	0..3580	2550..2650
5	портал О4 1860×2450 без заполнения (D2), откосы 420 — штукатурка, C1, без наличника (D21)	590..2450	0..2450
6	пенал К-01 (боковина у 0..580) h 2400	0..580	0..2400
7	экран 80" F32 (опущен); полотно у 635..2406, изображение +1254..+2250, плоскость х=150	635..2406	1254..2550
8	Р-К14 розетка	3200	300
9	Р-К16 экран (в нише)	2550	2600
10	LV11 Zigbee/триггер экрана	2550	2600
11	плинтус M02 h 120	3015	60

Балкон — W2 (сторона балкона) с порталом

с балкона на восток: слева у=45, справа у=3068 М 1:25

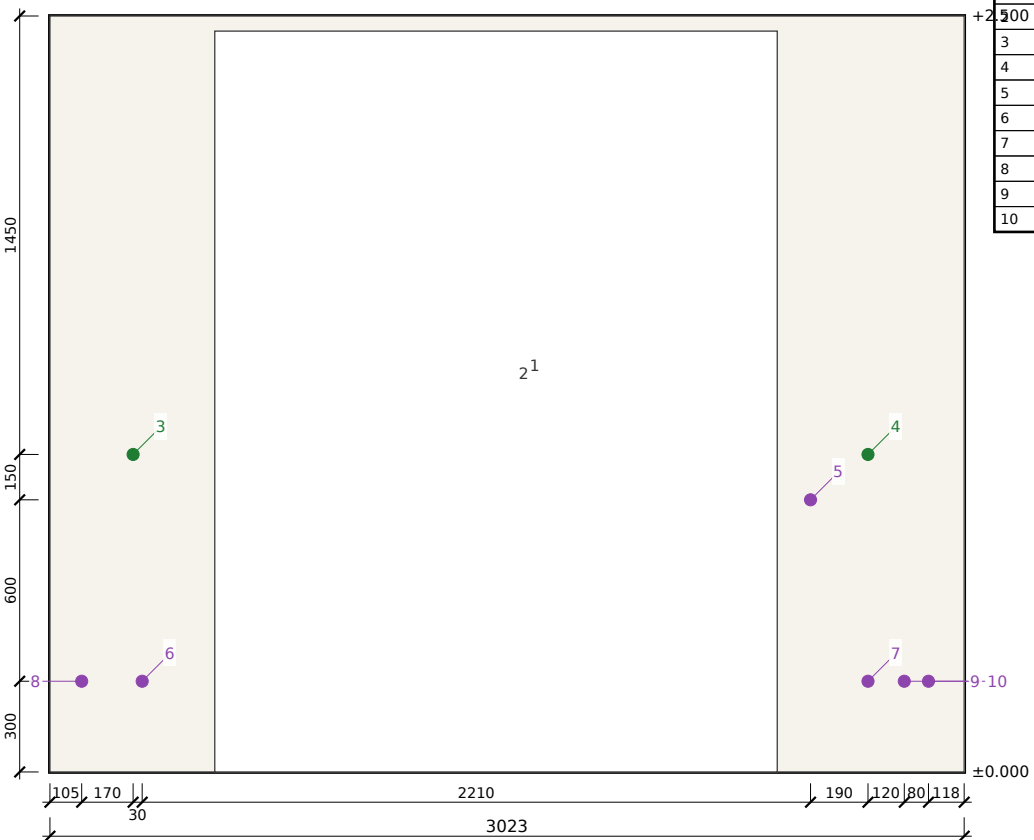


Отделка: штукатурка, Q3, C6 глубокоматовая; плинтус МДФ h 80 C6

№	Элемент	s, мм	z, мм
1	W2 фасадная кладка: утепление не требуется (внутренняя стена тёплого контура) — штукатурка + C6	45..3068	0..2500
2	портал О4 (со стороны балкона) — откосы C6	590..2450	0..2450
3	LV09 колонка R	320	1050
4	LV10 колонка L	2750	1050
5	S4 + T3 + ZB-2	2560	900
6	Р-В06 конвектор KV1	350	300
7	Р-В07 конвектор KV2	2750	300
8	Р-В03	150	300
9	Р-В04	2950	300
10	Р-В05	2870	300

Балкон — остекление В1 с приточными клапанами SV1/SV2

на запад: слева у=3068, справа у=45 М 1:25

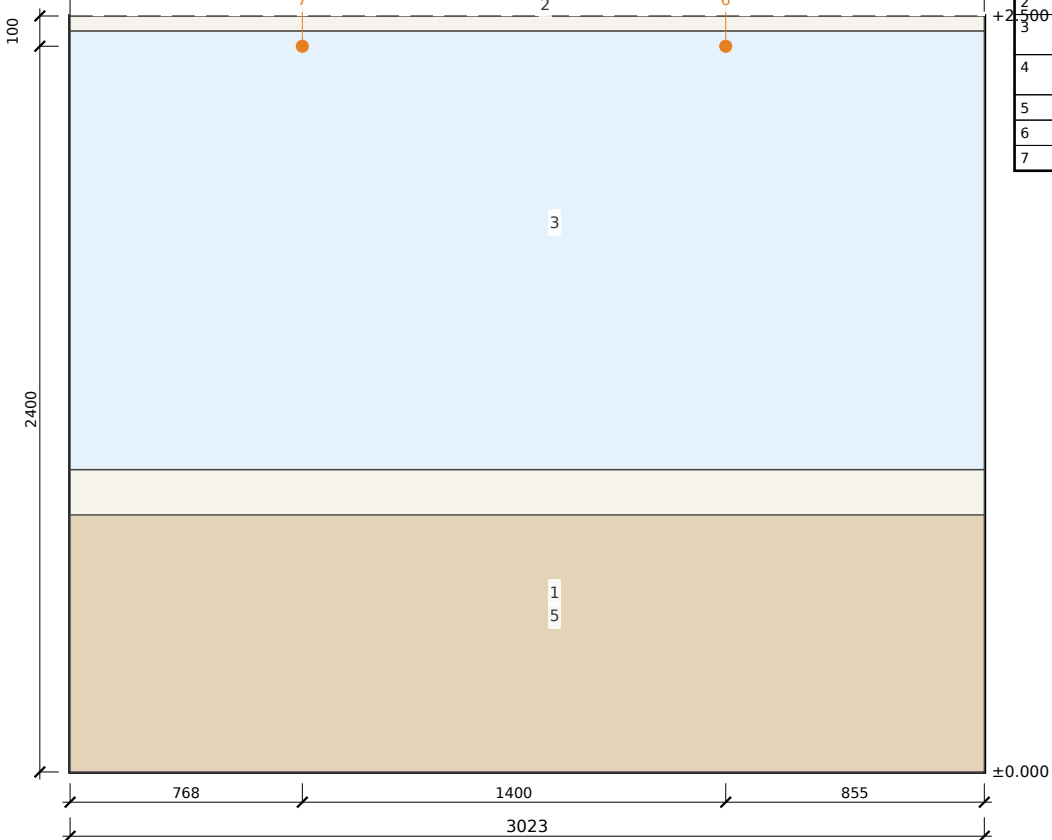

Отделка: паранет ГВЛ + C6; клапаны SV1/SV2 — заказ вместе с остеклением

№	Элемент	s, мм	z, мм
1	паранет: PIR/минвата 100 + пароизоляция + ГВЛ 12,5, C6 (0..+1000)	45..3068	0..1000
2	надоконная полоса +2450..+2500 C6	45..3068	2450..2500
3	тёплое остекление ПВХ 2-камерное, P2A (M32), +1000..+2450	45..3068	1000..2450
4	ниша шторы CN-3 150 (портьера на треке в 110 от стекла)	45..3068	2500..2600
5	П-диван F33 (спинка) h 850	45..3068	0..850
6	SV1 приточный клапан в верхней части рамы (K13)	900	2400
7	SV2 приточный клапан (K13)	2300	2400

КВ108-ДП-АР-11

Квартира №108, СПб, дизайн-проект

Изм.	Кол.уч	Лист	№док.	Подп.	Дата	Архитектурные решения	Стадия	Лист	Листов
Разраб.		rib-агенты			10.2026		Р	15	51
Пров.						Развертки стен. Кухня-гостиная и балкон Масштаб 1:25	ПИБ агенты rib-*		
ГИП									
Н.контр.									
Утв.									