


Прихожая — стена шкафа 2720 (фронт у=3121)

из прихожей на север: слева х=4740, справа х=7541 М 1:25

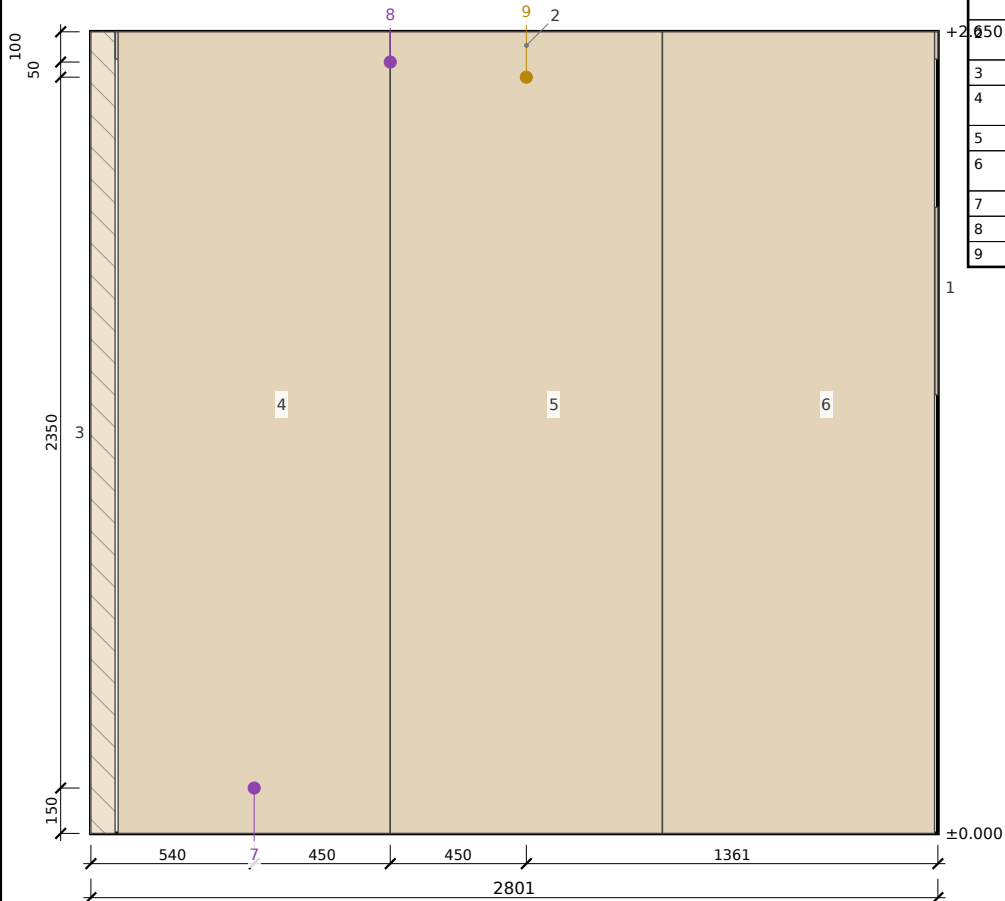

Отделка: фасады С2 (в цвет стены), пол перед шкафом: доска х<5910, керамогранит х>5910 (шов J2 по цоколю у=3171)

№	Элемент	S, мм	Z, мм
1	ЭЩ U15 (на W14, у 2245..2555) / СС-щит U16 (у 2650..3050) — на перпендикулярной стене, доступ свободен	7531..7541	1450..2070
2	доборы 10 к W12/W14, планка до потолка +2650 (шкаф h 2700 → 2650, D19)	4820..7541	2560..2650
3	торец W12 (х 4820) — краска С2	4740..4820	0..2650
4	шкаф F60 900: ниша робота h 400 без фасада, 2 двери 450 (С2 с рамкой-филенкой, М17)	4830..5730	0..2650
5	шкаф F61 900: 2 двери 450 + антресоль	5730..6630	0..2650
6	шкаф F62 900: дверь-зеркало 450 + дверь 450, отсек самоката	6630..7530	0..2650
7	Р-Н01 станция робота (в нише F60)	5280	150
8	Р-Н04/Р-Н05 БП (антресоли)	5730	2550
9	L18 подсветка шкафа (внутри)	6180	2500

						КВ108-ДП-АР-12			
						Квартира №108, СПб, дизайн-проект			
Изм.	Кол.уч	Лист	№док.	Подп.	Дата	Архитектурные решения	Стадия	Лист	Листов
Разраб.		рпб-агенты			10.2026		Р	16	51
Пров.						Развертки стен. Прихожая и коридор Масштаб 1:25	ПИБ агенты рпб-*		
ГИП									
Н.контр.									
Утв.									