



из помещения на юг ($-Y$): слева $x=7541$, справа $x=4900$ М 1:25

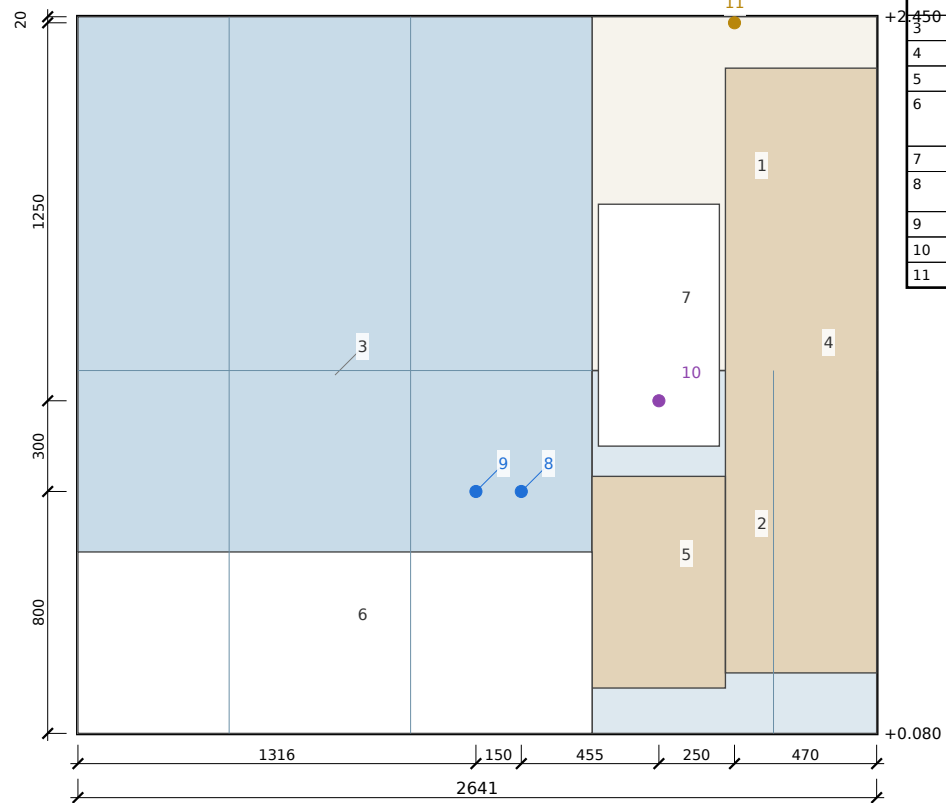

Отделка: гидроизоляция обмазочная: за ванной до потолка, остальное — 200 над полом ванной; плитка М21; краска С2 влагостойкая выше +1280


из помещения на север (+Y): слева $x=4900$, справа $x=7541$ М 1:25

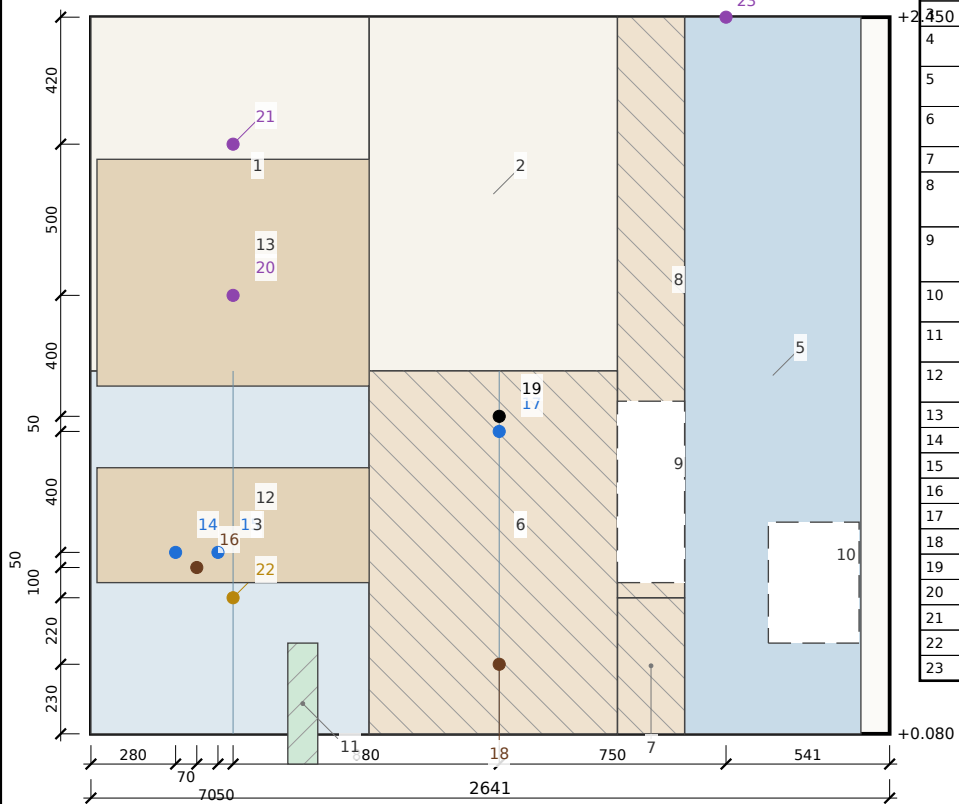

Отделка: ГИ 200 над полом; в душе (грань U10 y=5516) — до потолка; плитка до +1280 / в душе до потолка; краска выше


№	Элемент	S, мм	Z, мм
1	акриловая краска C2 класс 1	4900.5841	1280.2450
2	планка опорного шва +1280 (h 1200 от пола ванной) + дублирующий профиль	4900.5841	80.1280
3	плитка до потолка (за ванной, мокрая зона)	5841.7541	80.2450
4	печал подвесной F73 500x350	4900.5400	280.2280
5	корзина F74 440x350	5400.5841	230.930
6	ванна F66 1700x750, борт +600 от пола ванной, экран пластиковый (на W13 – торце/примыкания, герметик + уголок)	5841.7541	80.680
7	полотенцесушитель F75 400x800	5420.5820	1030.1830
8	водорозетка ХВС смесителя ванны (открытый монтаж, К-03)	6075	880 (h 800)
9	водорозетка ГВС	6225	880 (h 800)
10	P-V03 скрытый вывод полотенцесушителя IP44	5620	1180 (h 1100)
11	карниз 40 (над х 4900.5841)	5370	2430

из помещения на восток (+X): слева $y=3800$, справа $y=5841$ М 1:25

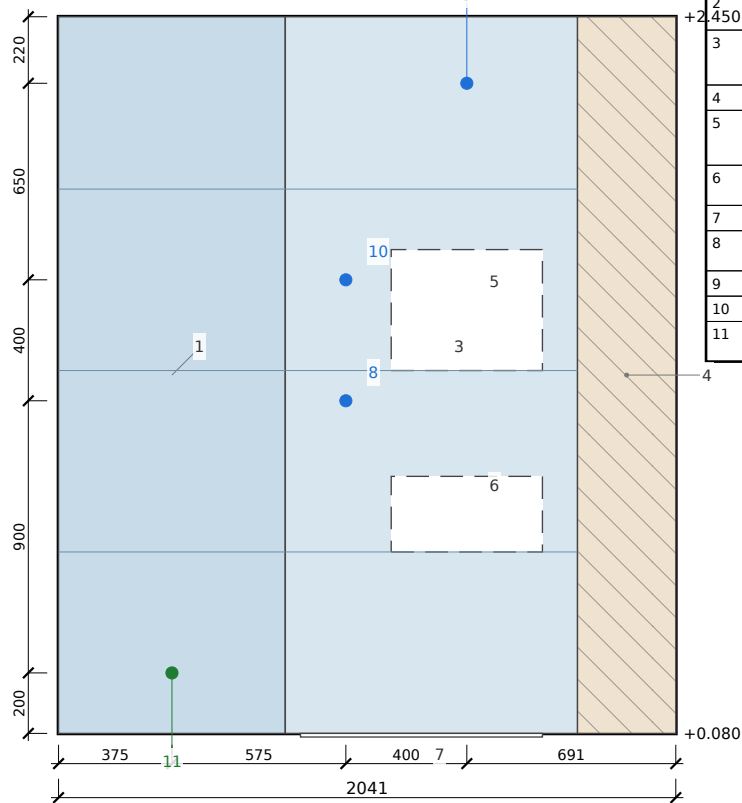

Отделка: гидроизоляция обмазочная на всю высоту (душ и за ванной); плитка M21, эпоксидная затирка

из помещения на запад (–X): слева $y=5841$, справа $y=3800$ М 1:25

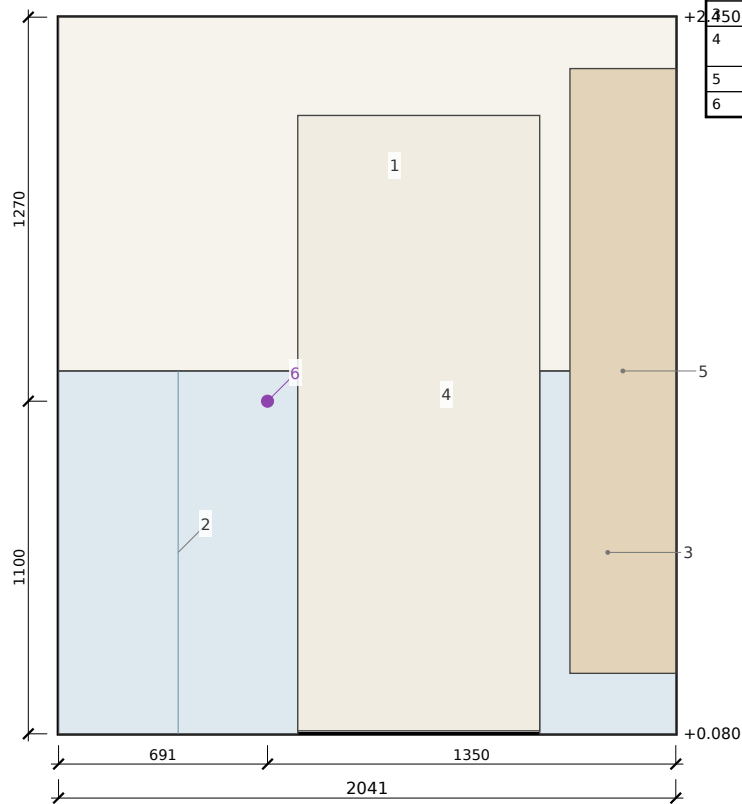

Отделка: ГИ 200 над полом ванной, заведена на откос и под коробку D3; плитка до +1280; краска

№	Элемент	5, мм	2, мм
1	Плитка до потолка — торцев ванны (горизонтально 1200х600, подрезка 750)	3800.4550	80.2450
2	Плитка до потолка — торцев ванны (горизонтально 1200х600, подрезка 750)	3800.4550	80.2450
3	Плитка горизонтально 1200х600, одна плитка на ширину 966 (без вертикальных швов)	5500.5516	80.2450
4	Облицовка ВС-12 = 95 (ПГ 6027 + 2хГВЛВ/СП 12.5 + ГВ + плитка), с W14 и потолку, без крепления в пазах торцев у=4550 — 95, плитка с загибом 45°	5500.5516	80.2450
5	короб U10 (грав. у=5516 — см. W15)	5516.5841	80.2450
6	ниша верхняя 500х400, глубина 70 (в облицовке), дно на опорном шве, уклон дна 2° к шову, латунный уголок С8	4900.5400	1280.1680
7	ниша нижняя 500х250, глубина 70, дно на шве +600 от пола ванной	4900.5400	680.930
8	линейный трап 800 мм облицовки, решетка +68.6	4600.5400	68.80
9	термостат скрытого монтажа (накладка 160) — ось у 4750 (перенос с — 5000) + вход в ящик, ячея ниш	4750	1180 (н 1100)
10	верхний душ — хромированный из облицовки, ось ниш	5150	2230 (н 2150)
11	ложка — штанга/держатель	4750	1580 (н 1500)
12	Нв ревизия сифона ванны 300х300 в экране (торец справа)	4175	280

№	Элемент	S, мм	Z, мм
1	краска С2 влагостойкая	3800.5841	1280.2450
2	плитка до +1280	5050.5841	80.1280
3	плитка до +1280 (за пеналом)	3800.4250	80.1280
4	D3 700x2010, коробка 800, верх коробки +2125 (2045 от пола ванной); порог-ступенька +90	4250.5050	90.2125
5	пенал F73 (торец)	3800.4150	280.2280
6	PV02 розетка фена IP44 (NW8)	5150	1180 (h 1100)

						КВ108-ДП-АР-13			
						Квартира №108, СПб, дизайн-проект			
Изм.	Кол.уч	Лист	№док.	Подп.	Дата	Архитектурные решения	Стадия	Лист	Листов
Разраб.		rib-агенты			10.2026		Р	17	51
Пров.									
ГИП						Развертки стен. Санузел основной. Раскладка плитки Масштаб 1:25	ПИБ агенты rib-*		
Н.контр.									
Утв.									