


Спальня — W2: буазери на месте зашитоого O1

из спальни на запад: слева $y=8911$, справа $y=3721$ М 1:25

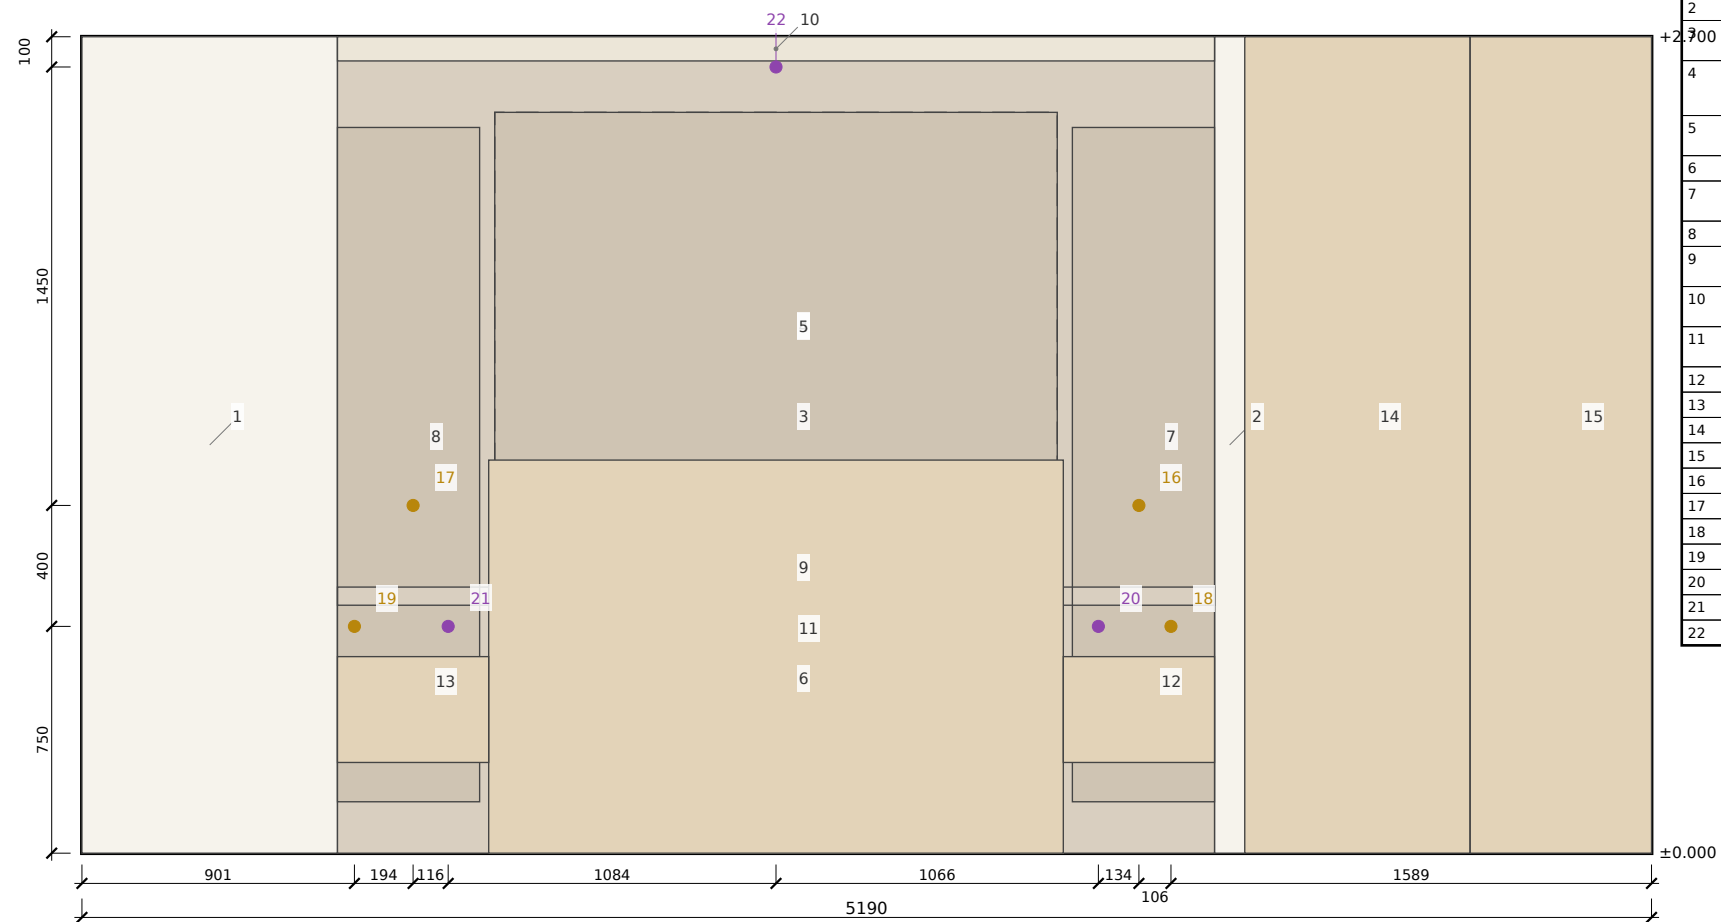


Отделка: буазери M06 C3; стены C2; ось композиции $y=6616$ = ось кровати = ось ТВ

№	Элемент	s, мм	z, мм
1	краска C2 класс 2	8066.8911	0.2700
2	краска C2 (простенок 5066.5166)	5066.5166	0.2700
3	бушера M06: МФФ 16-19 на стене и кармаше зашивки O1, изиль C3, рамки-молдинги 30	5166.8066	0.2700
4	зашивка O1 (каркас в откосе, минвата 100, парозащита, 2xTKL — заподлицо со стеной) — узел 8	5686.7546	850.2450
5	центральная верхняя филёнка 1860x1600 — СЛЕМАЯ на климмерх (= проём O1)	5686.7546	850.2450
6	центральная нижняя филёнка 1860, +170, +800	5686.7546	170.800
7	боковые филёнки 470 (верх +900, +2400, низ +170, +800)	5166.5636	170.2400
8	боковые филёнки 470	7596.8066	170.2400
9	посл-рейка на +850 (линия подоконника O1), цоколь 0.120, фриз +2450, +2600	5166.8066	820.880
10	карниз бушера с теневым пазом LED L9 (2700 K), +2620, +2700	5166.8066	2620.2700
11	кроват F42, мягкое изголовье h 1150.1300 (y 5666.7566)	5666.7566	0.1300
12	тумба F43 подвесная +300, +650	5166.5666	300.650
13	тумба F44	7566.8066	300.650
14	шкаф F46 (торец, до +2700)	4321.5066	0.2700
15	шкаф F45 (торец)	3721.4312	0.2700
16	бра L11-1 (P-R14)	7436	1150
17	бра L11-2 (P-R15)	7816	1150
18	56/57/59 рамка у тумбы	5310	750
19	58/510 рамка	8010	750
20	P-R01 + USB	5550	750
21	P-R02 + USB	7700	750
22	P-R10 БП LED (съемный ящик у карниза)	6616	2600

Спальня — W7: ТВ-зона по осі y=6616

из спальни на восток: слева $y=3721$, справа $y=8911$ М 1:25

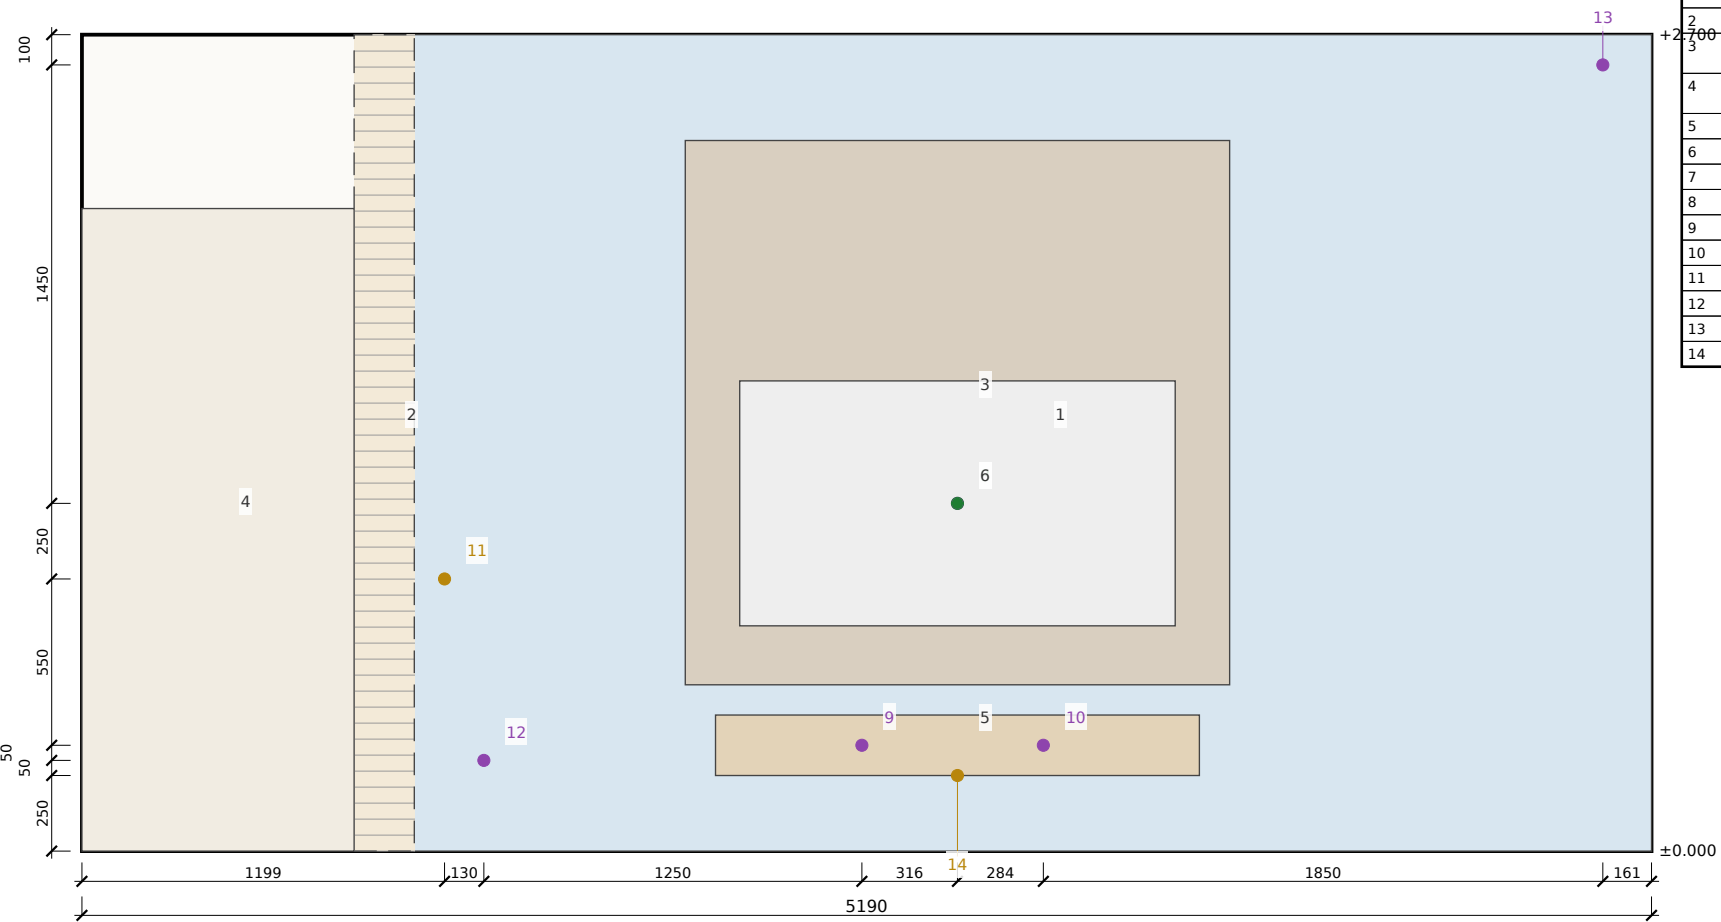

Отделка: ГКЛ-облицовка + Q4 + C2; рамка тон-в-тон

№	Элемент	В, мм	Г, мм
1	облицовка В7 ГКЛ 12,5 на клею/профиле (-40) у 4820.8911 – кабель ТВ/SS без штроб (N57), D23	4820.8911	0.2700
2	доброт ГПП 199 (у 4621.4820)	4621.4820	0.2700
3	рамка-молдинг 30 тон-тон С2 вокруг ТВ-зоны 1800х1800	5716.7516	550.2350
4	D1800х2100, коронка 900, верх +2125; над дверью 4820.8911 и стена до +2700	3721.4621	0.2125
5	консоль подвесная F47 I600х300, +250...+450	5816.7416	250.450
6	ТВ Б5 F48, центр +1150	5896.7336	745.1555
7	P.R03 x2 за ТВ (ниша/закладная)	6616	1150
8	L.V02/L.V03/L.V04 R45, ТВ, HDMI-рофра	6616	1150
9	P.R04 в консоли	6300	350
10	P.R12 БП подсветки консоли	6900	350
11	S5 проходной 2-кл.	4920	900
12	P.R07	5050	300
13	P.R11 БП LED карниза	8750	2600
14	L12 подсветка под консолью	6616	250

						КВ108-ДП-АР-15			
						Квартира №108, СПб, дизайн-проект			
Изм.	Кол.уч	Лист	№док.	Подп.	Дата	Архитектурные решения	Стадия	Лист	Листов
Разраб.		rib-агенты			10.2026		Р	19	51
Пров.									
ГИП						Развертки стен. Родительская спальня Масштаб 1:25	ПИБ агенты rib-*		
Н.контр.									
Утв.									