


Узел 1а. Примыкание ГКЛ-потолка к стене, спальня/детская +2700


М 1:10 (схематично, по detail¹с.md)

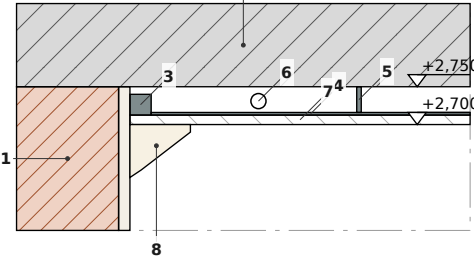

1. Стена (кладка/ж/б) + штукатурка
2. Плита перекрытия, низ +2750
3. ПН 28/27 по демпферной ленте, дюбели в стену шаг 400
4. ПП 60/27, низ +2712,5
5. Прямой подвес, шаг 600
6. Гофра нг ≤ Ø20 в зазоре 37,5 (D15)
7. ГКЛ (ГСП-А) 12,5, низ +2700; серпянка, шпаклёвка, окраска С1
8. Карниз M04 80×70: клей только к стене, к потолку — акриловый герметик 3 мм

Узел 1в. Ванная/постирочная: теневое примыкание ГКЛВ к плитке


М 1:10 (схематично, по details.md)

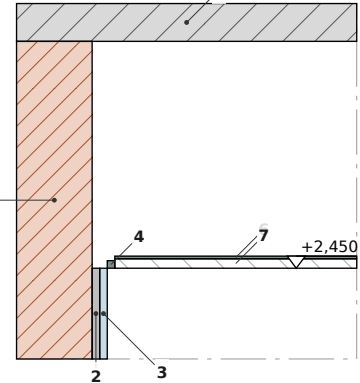

1. Стена/перегородка
2. Гидроизоляция + клей C2TE S1
3. Плитка стены до потолка
4. Теневой профиль 10×10 под окраску, на клею-герметике поверх плитки
5. Плита перекрытия
6. ПП 60/27 оцинк. на подвесах (пленум 300/250: EF1/EF2)
7. ГКЛВ 12,5, низ +2450 (ванная) / +2500 (постирочная); шов 10 — тень

Узел 3. Люк-невидимка Н1/Н3 в коробе (сечение в плане)


М 1:10 (схематично, по details.md)

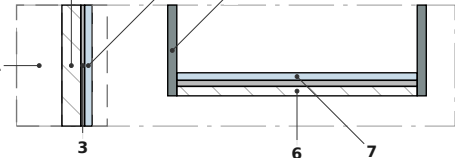

1. Полость короба стояков (узел Н1/Н2)
2. Короб: ПП 60/27 + 2×ГВЛВ 12,5
3. Клей C2TE S1
4. Плитка/«кабанчик»; швы совпадают с контуром люка
5. Алюминиевая рама люка к каркасу короба
6. Полотно ЦСП/ГВЛВ 12,5 на магнитно-нажимных защёлках (push), уплотнитель
7. Облицовка полотна той же плиткой; по контуру — силикон в тон (зазор 2)

Узел 5. Порог-ступень ванной D3 (J5, D20)


М 1:10 (схематично, по details.md)

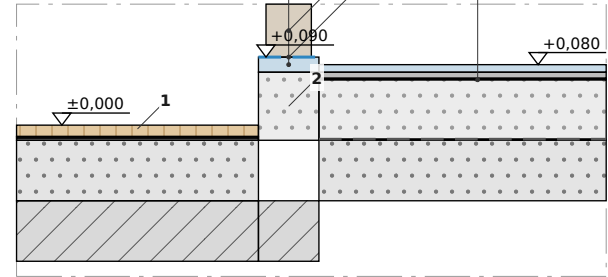

1. Коридор: Р-ОАК, доска ±0
2. Основание порога — ЦПС по нижней гидроизоляции
3. Ступень-порог керамогранит С9 20, верх +90; фаска + контрастная полоса
4. Гидроизоляция подиума заведена на порог, под коробку и на откосы на 200
5. Коробка D3 на пороге (верх +2125), полотно низ +110
6. Ванная: Р-BATH, пол +80 (порог на 10 выше — ограничитель воды)

Узел 1б. Потолок кухни, прихожей, коридора +2650 (пленум 100), спот


М 1:10 (схематично, по detail¹с.md)

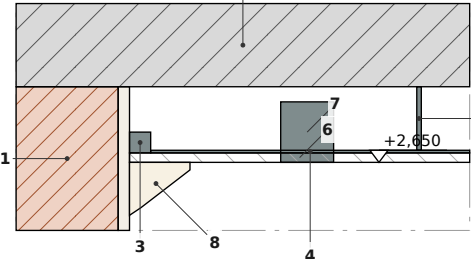

1. Стена + штукатурка
2. Плита перекрытия, низ +2750
3. ПН 28/27 по демпферной ленте
4. ПП 60/27 на подвесах с тягой, низ +2662,5
5. Подвес с тягой
6. ГКЛ 12,5, низ +2650 (без перепада на границе кухня/прихожая)
7. Встроенный спот L2/L15/L16, монтажная глубина ≤ 80 (пленум 87,5)
8. Карниз 80×70 (к стене)

Узел 2. Ниша под карниз штор CN-1/CN-2 (+2700, глубина 62)


М 1:10 (схематично, по detail¹с.md)

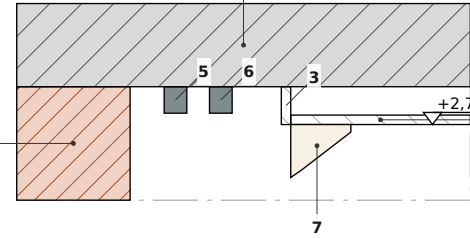

1. Наружная стена W1 (откос окна)
2. Плита; дно ниши — шпаклёвка + С1
3. Борт ниши ГКЛ 12,5 на ПН/ПП, вертикальная грань 62
4. Потолок ГКЛ +2700
5. Трек ряд 1 (блэкаут) ≤ 35, ось 60 от W1, дюбели в плиту
6. Трек ряд 2 (тьюль), ось 120 от W1
7. Карниз M04 по кромке ниши (у 8711)

Узел 4. Стык доска/керамогранит J2 (и шов J4 у дверей D1/D2)


М 1:10 (схематично, по details.md)

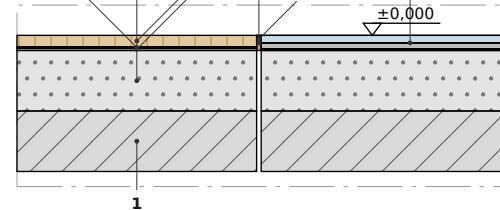

1. плита перекрытия (верх), верх -100
2. стяжка с водяным ТП застройщика (существующая, не трогать) — 80
3. грунт + локальный ремонтный состав (до 3) — 3
4. клей MS-полимер эластичный (зубчатый шпатель В11) — 2
5. инженерная доска 2-слойная 15 (90×600, ёлочка 1:6) — 15
6. Справа: Р-TILE-HALL — грунт, ремонтный состав 2; клей C2TE S1 (эластичный, для ТП) 8; керамогранит 600×600×10 ректифицикат 10
7. Пробковый компенсатор 5 на всю толщину покрытия
8. Латунная вставка С8 3×10 заподлицо, на эпоксидном/MS-клею, без саморезов

Узел 6. Гидроизоляция ванной (Р-BATH) и рамка-бортик коллектора U14

М 1:10 (схематично, по details.md)

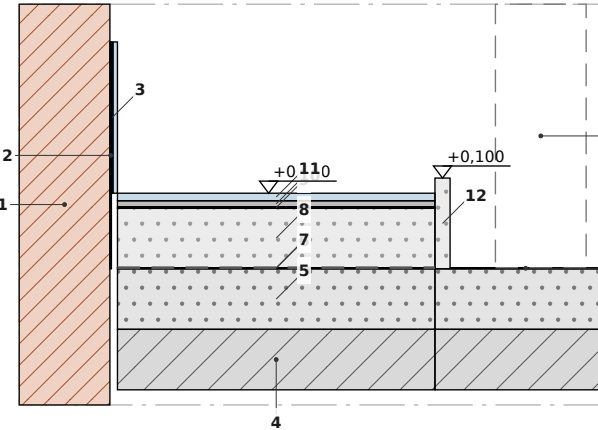

1. Стена ванной
2. Нижняя ГИ: заход на стену 200 над полом ванной (до +280)
3. Основная ГИ 2 слоя: заход 200; в душе и за ванной — до потолка +2450
4. плита, верх -100
5. стяжка с водяным ТП (сущ.), верх -20 — не резать (D3/D4) — 80
6. грунт + нижняя обмазочная гидроизоляция (барьер над ТП и техподпольем), заход 200 над чистым полом — 1,5
7. демпферная лента 10 по периметру; трубы Ø50 трапа/ванны — на стяжке, защитный слой ≥ 30
8. подиум ЦПС М300 фиброармированная + сетка 50×50 Вр4; в душе уклон 1,5 % к трапу — 78,5
9. основная обмазочная гидроизоляция 2 слоя, ленты, манжета/фланец трапа, вклейка в рамку U14 — 2
10. клей C2TE S1 + мат TP1 (вне ванны, душа, коробов; ≥ 100 от рамки U14) — 8
11. керамогранит 10 (60×60 сухая зона, 60×120 душ R10/В) — 10
12. Бортик ЦСП 20 / нерж. уголок, на клею к стяжке, верх +100; без анкеров
13. Ниша коллектора: подиум не заливается, дно — стяжка с нижней ГИ
14. Коллектор U14 (h ≈ 400), доступ через съёмный цоколь тумбы F71

						КВ108-ДП-АР-17		
						Квартира №108, СПб, дизайн-проект		
Изм.	Кол.уч	Лист	№док.	Подп.	Дата	Архитектурные решения	Стадия	Лист
Разраб.		риб-агенты			10.2026		Р	21
Пров.						Узлы 1-6: потолки, ниши штор, люки, стыки покрытий, порог ванной, гидроизоляция Масштаб 1:10	ПИБ агенты rib-*	
ГИП								
Н.контр.								
Утв.								