



Фрагмент 1. Ванная R5 (1:25)

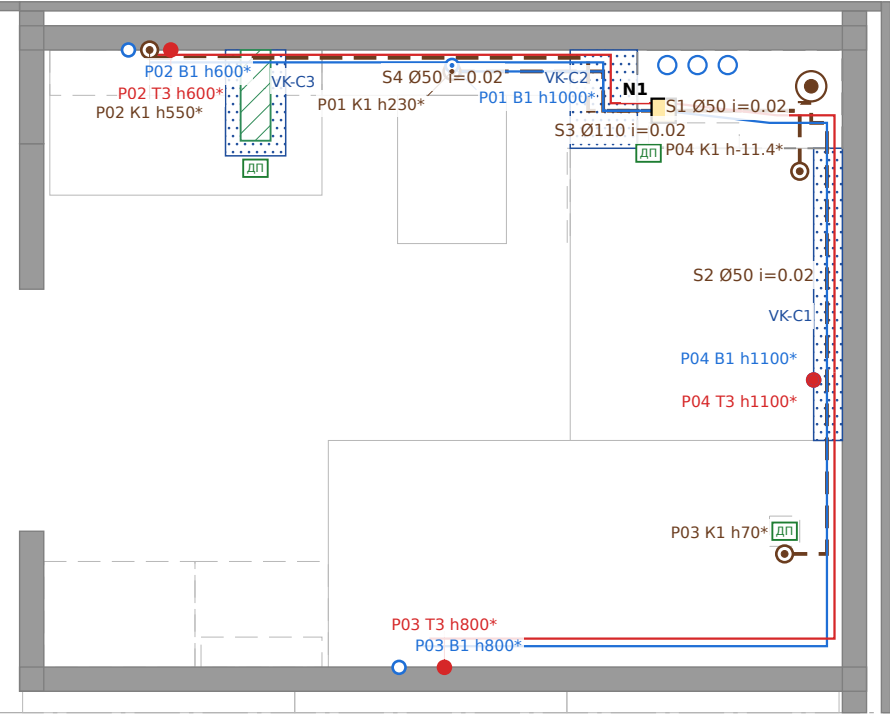

Фрагмент 2. Постирочная R6 и мойка кухни (1:25)

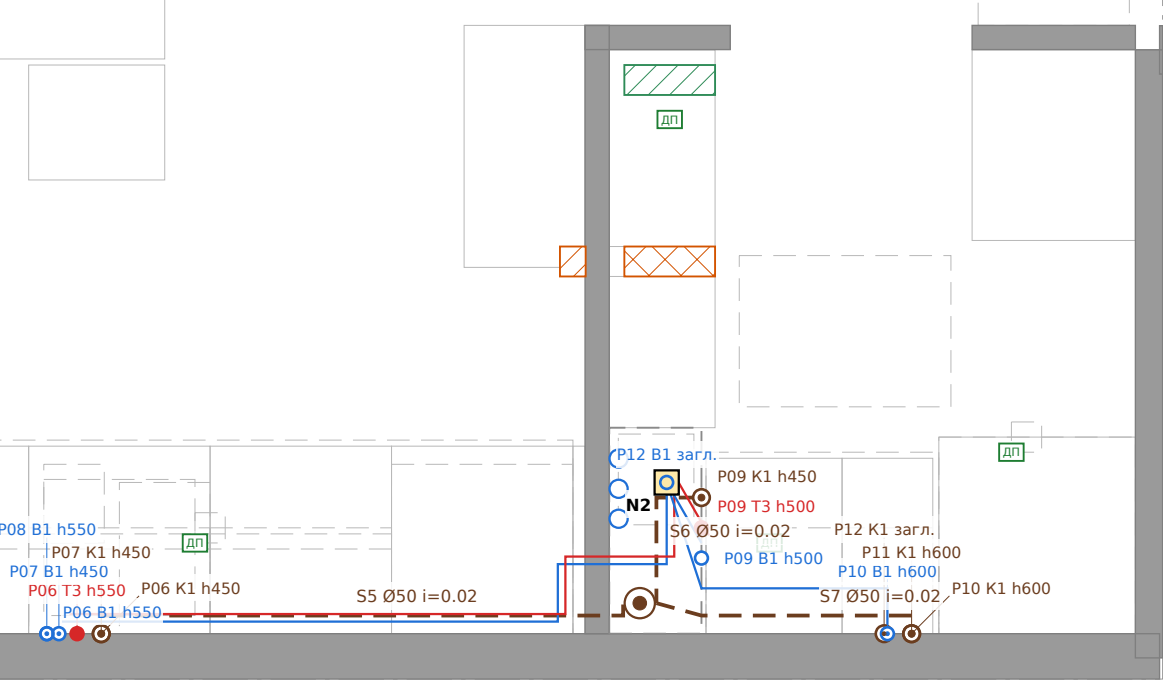

Канализация: уклоны и отметки лотка (мм от УЧП)

Уч.	Прибор / трасса	Стояк	Ø	i	L, м	Δh	z нач.	z кон.	ОК
S1	P04 душ: низкий линейный трап у облицовки W14 (выпуск у сев...	U6	50	0.02	0.26	5.3	-12.7	-18	да
S2	P03 ванна: сифон у правого торца (x≈7350) → под ванной → в ...	U6	50	0.02	1.68	33.7	15.7	-18	да
S3	P01 унитаз подвесной (инсталляция, ось х 6250)	U6	110	0.02	1.26	25.3	7.3	-18	да
S4	P02 раковина в тумбе 900 (выпуск +550 от пола ванной)	U6	50	0.02	2.31	46.2	28.2	-18	да
S5	P06 мойка кухни (+ ПММ через сифон мойки)	U1	50	0.02	1.77	35.3	17.3	-18	да
S6	P09 хозяйка 450 (выпуск на грани короба U5)	U1	50	0.02	0.5	10.0	-8.0	-18	да
S7	P10 СМА (сифон в карго, + конденсат сушильной машины)	U1	50	0.02	0.85	17.0	-1.0	-18	да

Указания

— уклоны: Ø50 ≥ 0,02 (принято 0,02), Ø110 ≥ 0,012 (принято 0,02) — СП 30.13330.2020
— повороты — отводами 45°+45°, обратных уклонов нет; труба не ниже верха стяжки −20 (вертикальный спуск к тройнику — в коробе)
— в коробе U10 душ подключается в самую нижнюю точку (эксцентрический переход 110/50 с совмещёнными лотками), WC/ванна/раковина — сверху через косой тройник 110/110/45°
— в коробе U5: Ø110 короткий отвод от тройника стояка с ревизией → косой тройник 110/50 (кухня через W10) + эксцентрический переход 110/50 (постирочная)
Подиум ванной +80 ДОСТАТОЧЕН при лотке отвода тройника K1 U6 не выше 1.3 (душ — критический прибор). Расчётная отметка решётки трапа +68.6, низ корпуса трапа -1.4 (над стяжкой −20). Отметка лотка врезки неизвестна
— ВОПРОС НА ОБМЕР; при лотке +20 → подиум +100, +40 → +120, +60 → +140.

Чувствительность подиума к отметке врезки

Лоток тройника U6	Пол ванной треб.	Кухня/постир. ОК
-60	65	да
-40	65	да
-20	65	да
0	80	да
20	100	да
40	120	да
60	140	да

Требует обмера

— ОБМЕР (K-15/F-07): отметка лотка отводов тройников K1 U1 и U6 от УЧП (критерий: U6 ≤ +1 → подиум +80 и порог +90 по D20 без изменений; иначе подиум +100/+120 и порог поднимается соответственно) — до заказа трапа и материалов.
— ОБМЕР: назначение стояков U2–U4, U7–U9 (B1/T3/T4), диаметры отводов, наличие запорной арматуры застройщика.
— ВСКРЫТИЕ: положение вентканалов U25/U26 внутри коробов и ревизий K1.
— Есть ли выпуск Ø110 бывшего WC постирочной в полу (x=5079) и на какой отметке.
— Давление на вводе (манометр) — подтвердить необходимость редукторов (1 этаж — максимальное давление в стояке).
* В ванной R5 высоты — от чистого пола ванной (+80 к УЧП квартиры).

						КВ108-ДП-ВК-02			
						Квартира №108, СПб, дизайн-проект			
Изм.	Кол.уч	Лист	№док.	Подп.	Дата	Водопровод и канализация	Стадия	Лист	Листов
Разраб.		рпб-агенты			10.2026		Р	34	51
Пров.						Фрагменты 1:25: ванная, постирочная, мойка кухни — водопровод и канализация (уклоны) Масштаб 1:25			
ГИП									
Н.контр.									
Утв.									