


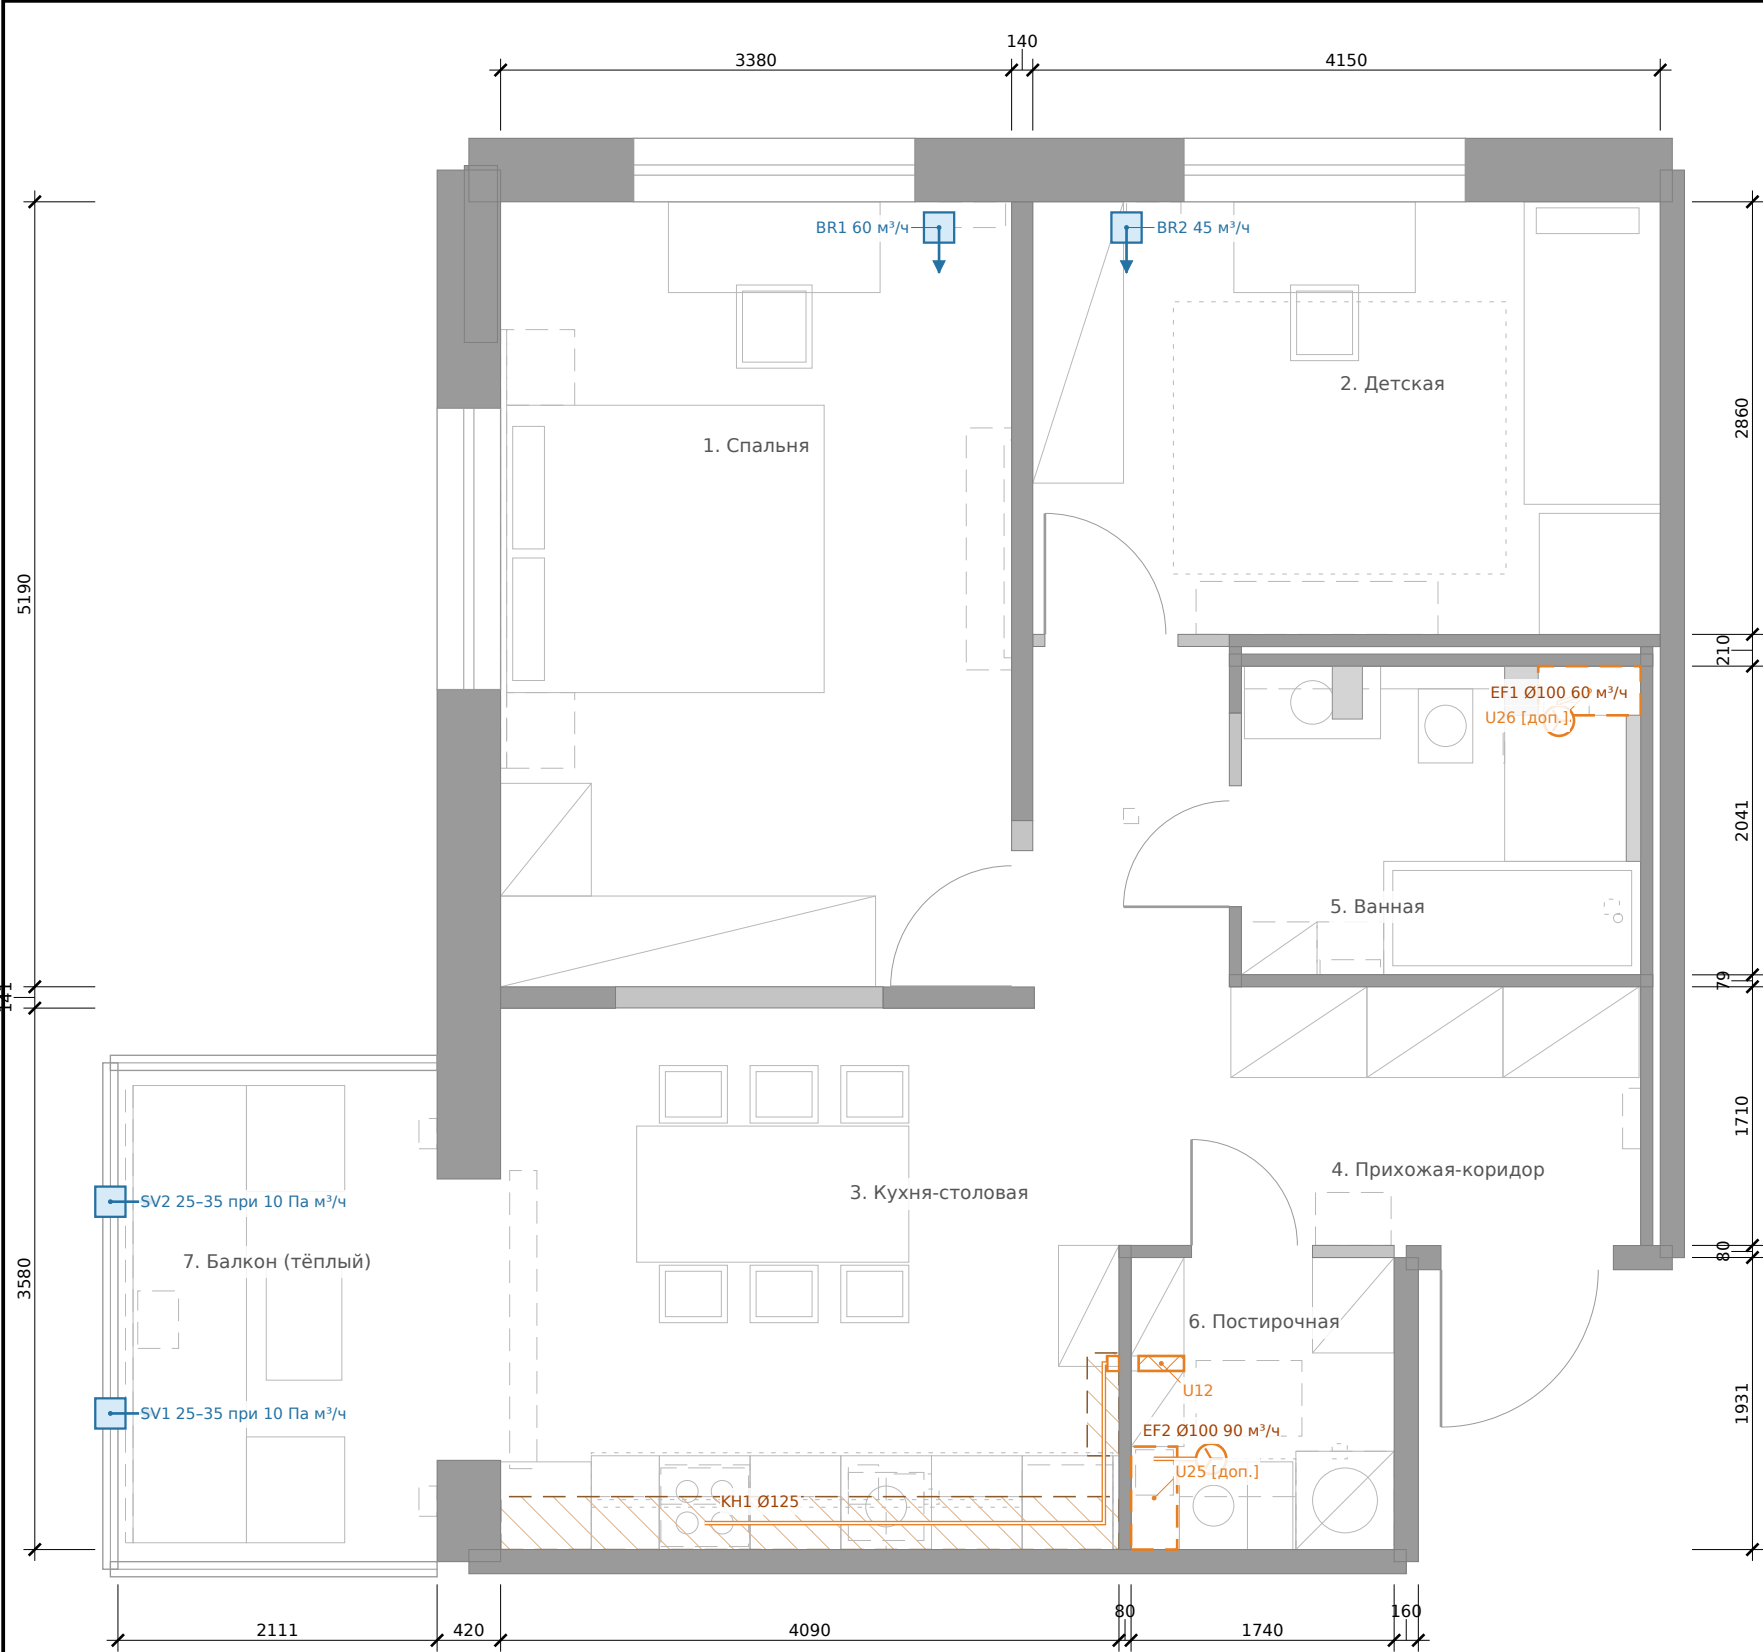

Условные обозначения

- Вентканал (существующий)
- Вентканал в коробе стояков [допущение D10]
- Вентилятор вытяжной с обратным клапаном
- Воздуховод (Ø по подписи)
- Бризер / приточный клапан, стрелка — приток
- Короб-опуск потолка под воздуховод

Воздушный баланс

Помещение	Норма	Расчёт, м³/ч	Устройство
R1 спальня	2 чел. x 30 = 60 м³/ч (или 3 м³/ч·м² x 17,54 = 53)	60	BR1
R2 детская	1 чел. x 30 = 30 м³/ч (3 x 11,87 = 36)	45	BR2
R3+R7 кухня-гостиная	компенсация вытяжки кухни	60 (естеств.) / до 350 при работе вытяжки	SV1, SV2 + микропротравливание окна балкона при готовке
R3 кухня (электроплита)	60		канал U12 через решётку U13 (естественная) + вытяжка КН1 в режиме готовки
R5 ванная совмещённая	50		EF1 + естественная через U26
R6 постирочная	25	90	EF2 + естественная через U25

Вытяжка

Марка	Оборудование	Воздуховод	Подключение
КН1	Вытяжка кухни встраиваемая 60 (F17) в вентканал U12 через р...	Ø125 круглый ПВХ/оцинк., гладкий, герметичные соединения (базовый); е...	выход вытяжки вверх в карниз (+2400...+2700) → вдоль W3 над навесными и пеналом холодильни...
EF1	Вентилятор вытяжной ванной (потолочный/канальный Ø100, ≥ 10...	Ø100 гладкий в подшивном потолке +2450...+2750 (УЧП); вентилятор над д...	врезка в канал U26 через стенку короба U10 на +2550...+2650 (выше +2450) после вскрытия ко...
EF2	Вентилятор вытяжной постирочной (потолочный/канальный Ø100,...	Ø100 в подшивном потолке +2500...+2750	врезка в канал U25 через грань короба U5 (у 560..680, выше люка Н3; свободно от навесных ...

Указания

Приток: бризеры в спальне и детской, оконные приточные клапаны в остеклении балкона (кухня-гостиная); перетекание через подрезы дверей. Вытяжка: естественная через 3 собственных вентканала + бытовые вентиляторы с обратными клапанами (ванная, постирочная) и вытяжка кухни в канал U12. ПВУ и воздуховоды по коридору НЕ требуются (бриф «вентиляция по потолку» реализуется короткими воздуховодами в подшивных потолках с/у и в карнизе кухни). Переток: подрез 15-20 мм дверей D1, D2 (спальня, детская), D3, D4 (с/у) — или переточные решётки; без этого бризеры не работают на вытяжку. Кондиционирование: кондиционирование НЕ предусмотрено (бриф); наружные корзины на фасаде отсутствуют (U21).

						КВ108-ДП-ОВ-02			
						Квартира №108, СПб, дизайн-проект			
Изм.	Кол.уч	Лист	№док.	Подп.	Дата	Отопление и вентиляция	Стадия	Лист	Листов
Разраб.		риб-агенты			10.2026		Р	36	51
Пров.									
ГИП						Вентиляция: трассы, бризеры, вытяжки Масштаб 1:50	ПИБ агенты риб-*		
Н.контр.									
Утв.									