


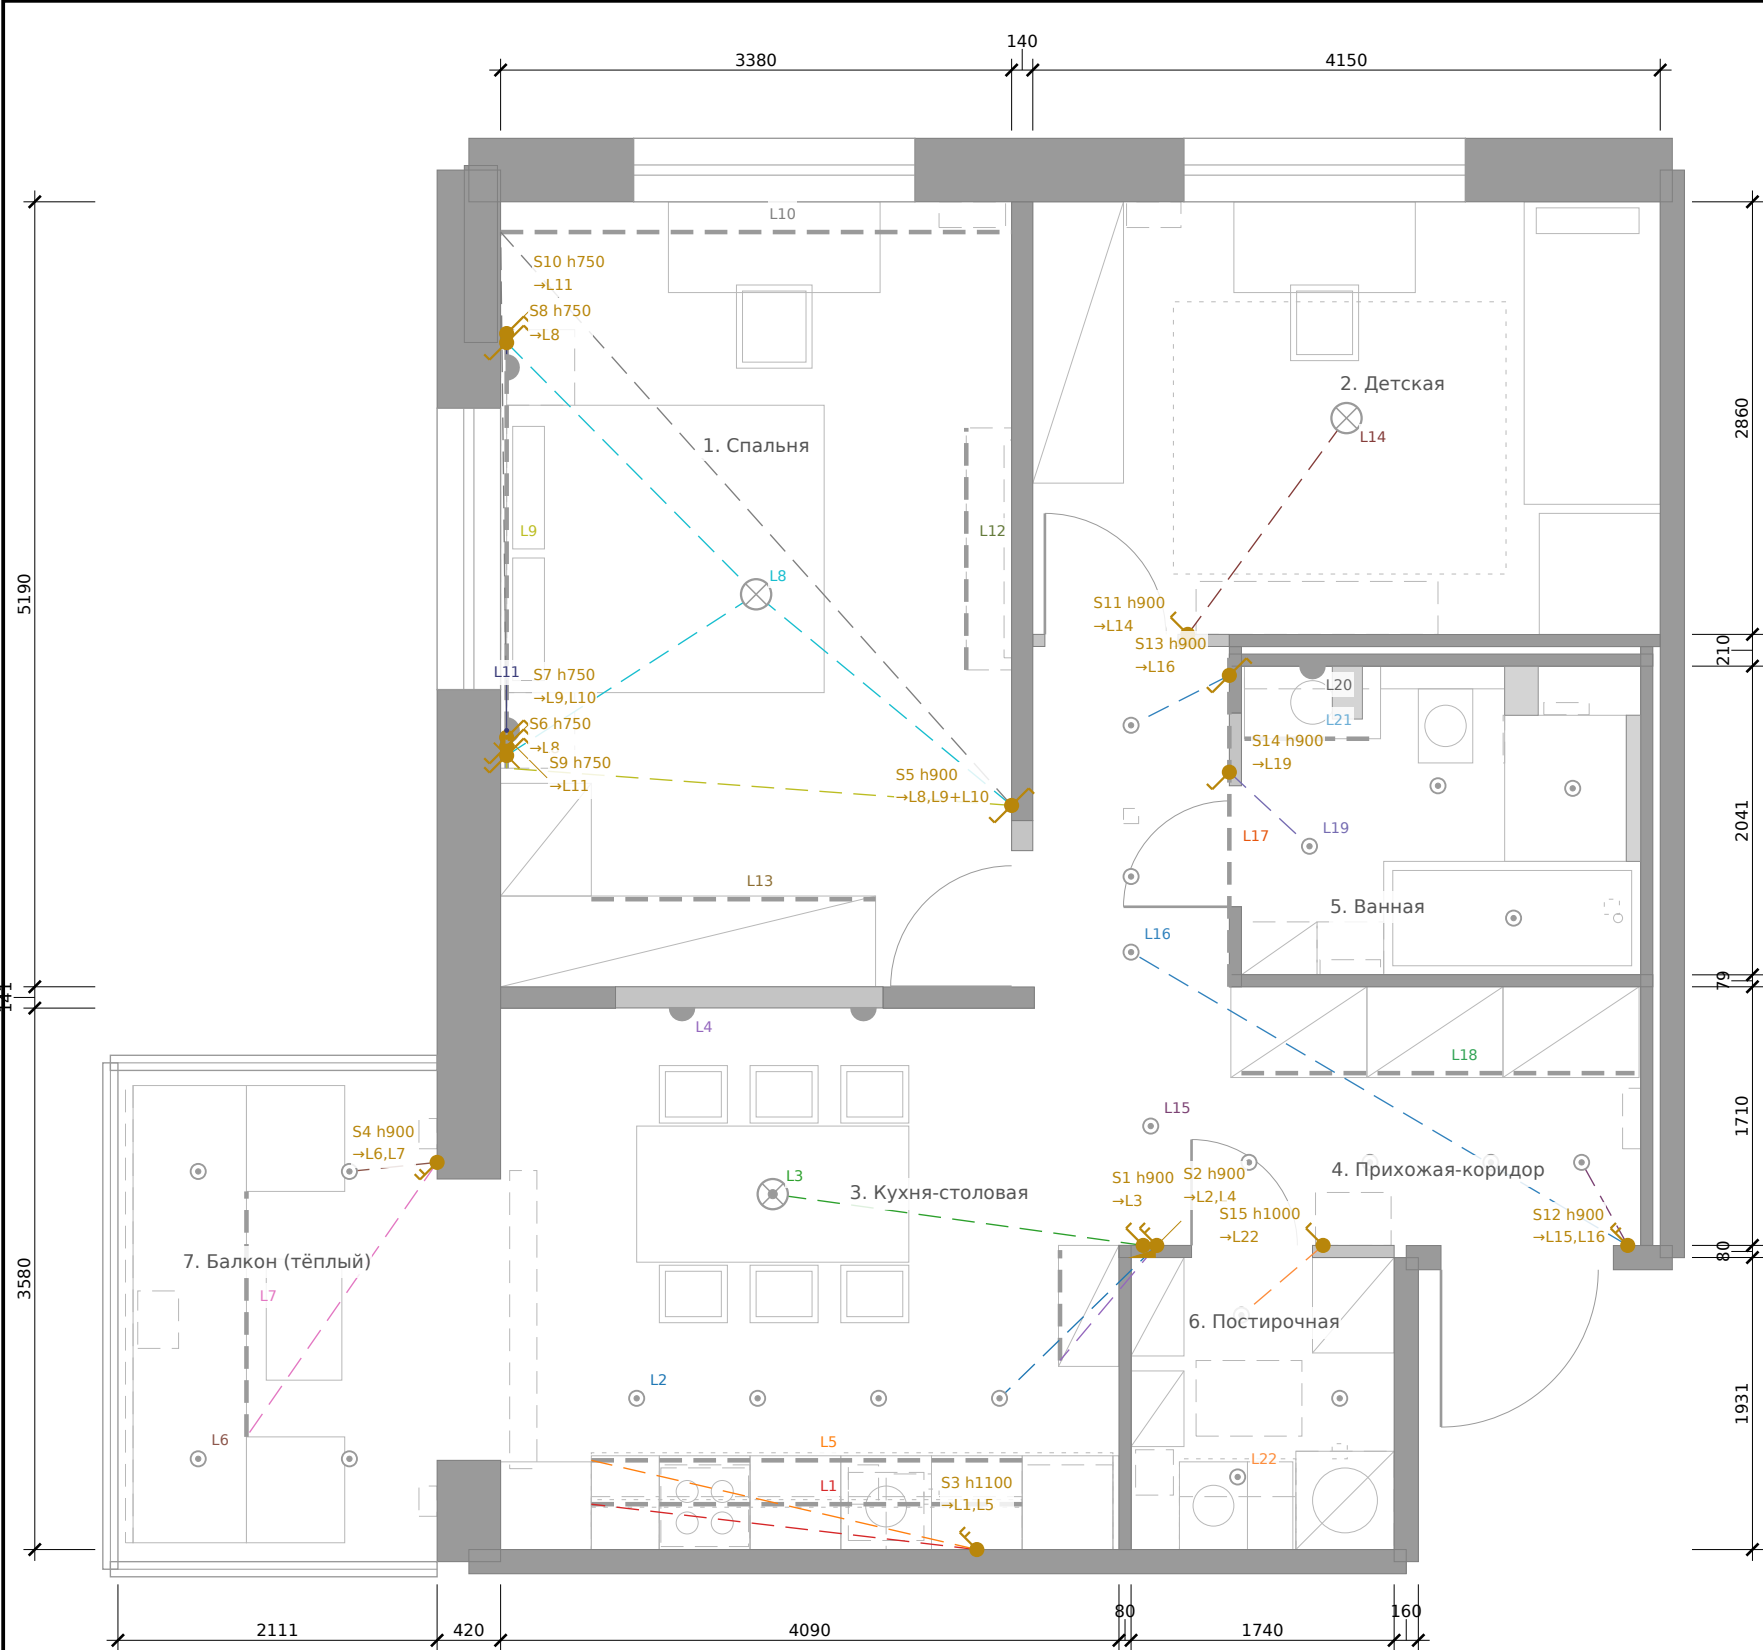

Условные обозначения (ГОСТ 21.614)

- Выключатель одноклавишный, скрытой установки
- Выключатель двухклавишный
- Выключатель проходной
- Выключатель перекрёстный
- Светорегулятор (диммер, Zigbee)
- Связь выключателя с группой (цвет — группа)

Ведомость выключателей

Марк а	Пом.	Тип	h	Управляет	Стена	Привязка, мм	Примечание
S1	R3	dimmer	900	L3: Столовая — люстра	W11 (сторона прихожей)	3291 от W14; 0 от W11	вход в кухню из прихожей; Zigbee-диммер (работает и без шлюза), рамка 3-местная S1-S2 + с...
S2	R3	2kl	900	L2: Кухня — споты; L4: Столовая — бра + буфет	W11	3201 от W14; 0 от W11	в одной рамке с S1; Zigbee-реле/диммеры за клавишами
S3	R3	2kl	1100	L1: Кухня — рабочая подсветка; L5: Кухня — цоколь (ночь/кино)	W3 (фартук)	940 от W10; 0 от W3	в рамке с розеткой P-K06 (фартук над ПММ)
S4	R7	2kl	900	L6: Балкон — споты; L7: Балкон — цоколь дивана	W2 простенок (балкон)	0 от W2; 608 от B2	Zigbee-диммеры; рядом терморегулятор ТП балкона T3 и кнопка «Кино» ZB-2
S5	R1	pass	900	L8: Спальня — люстра; L9+L10: Спальня — LED буазери + Спальня — LED карниз	W7 (облицовка ГКЛ)	0 от W7; 1200 от W8	у входа в спальню, 2-клавишный проходной: кл.1 — цепь L8 (с S6/S8), кл.2 — цепь L9+L10 (с...
S6	R1	cross	750	L8: Спальня — люстра	буазери F41 (сторона входа)	40 от W2; 1530 от W8	у кровати, рамка над тумбой F43
S7	R1	pass	750	L9: Спальня — LED буазери; L10: Спальня — LED карниз	буазери F41	40 от W2; 1590 от W8	у кровати, та же рамка
S8	R1	pass	750	L8: Спальня — люстра	буазери F41 (сторона окна)	40 от W2; 931 от W1	у кровати, рамка над тумбой F44
S9	R1	1kl	750	L11: Спальня — бра	буазери F41	40 от W2; 1650 от W8	бра L11-1 (сторона входа); L11-2 — S10
S10	R1	1kl	750	L11: Спальня — бра	буазери F41	40 от W2; 871 от W1	бра L11-2 (сторона окна)
S11	R2	dimmer	900	L14: Детская — потолочный	NW4 (у двери D2, со стороны ручки)	1025 от W7; 0 от NW4	Zigbee-диммер + беспроводной пульт ZB-4 у кровати (без штроб в W6/W1)
S12	R4	2kl	900	L15: Прихожая — споты; L16: Коридор — споты	W5 (у входной двери, сторона ручки)	86 от W14; 1 от W5	кл.1 — L15 прихожая; кл.2 — L16 коридор (проходной с S13); рядом кнопка «Уход» ZB-3
S13	R4	pass	900	L16: Коридор — споты	W12 (конец коридора у детской)	0 от W12; 191 от NW4	проходной, пара к S12 кл.2
S14	R4	1kl	900	L19: Ванная — споты + вентилятор	NW8 (коридор, у двери D3)	0 от NW8; 831 от NW4	свет ванной + вентилятор с таймером выбега; снаружи помещения; рядом терморегулятор T1
S15	R4	1kl	1000	L22: Постирочная — споты + вентилятор	NW9 (прихожая, у двери D4)	2101 от W14; 0 от NW9	свет постирочной + вентилятор с таймером; h 1000 — над банкеткой F63; рядом терморегулято...

Управление

кухня-столовая и балкон — Zigbee-диммеры/реле за проводными клавишами + сценарные кнопки и шлюз в U16 (сцены сонсерт п.5: Утро, Ужин, Кино, Вечер, Ночь, Уход); прочие помещения — классическая проводная схема; свет работает без шлюза

Сцены:

Утро: L1 100 %, L3 60 %, L11 40 %, L9 30 %, L14 60 %, L16 70 %

Ужин/гости: L3 80 %, L4 60 %, L1 30 %, L6 30 %, L7 on

Кино: шторы F37 закрыть, экран F32 вниз (Zigbee + 128-триггер проектора), L6 → 0 за 10 с, L7 5-10 %, L5 5 %, L1-L4 off

Вечер: L3 40 %, L6 40 %, L9 60 %, L11 50 %, L14 30 %, L16 40 %

Ночь: всё off; L12, L17, L21 — по датчикам движения 5-10 %

Уход: весь свет off, краны LV17/LV18 закрыть, контроль протечек и датчиков открытия

Высоты h — до центра изделия от УЧП ±0.000; привязки — до грани ближайшей стены по X и по Y, мм.

						КВ108-ДП-ЭО-02			
						Квартира №108, СПб, дизайн-проект			
Изм.	Кол.уч	Лист	№док.	Подп.	Дата	Электроосвещение	Стадия	Лист	Листов
Разраб.		риб-агенты			10.2026		Р	29	51
Пров.									
ГИП									
Н.контр.						План выключателей Масштаб 1:50	ПИБ агенты риб-*		
Утв.									