


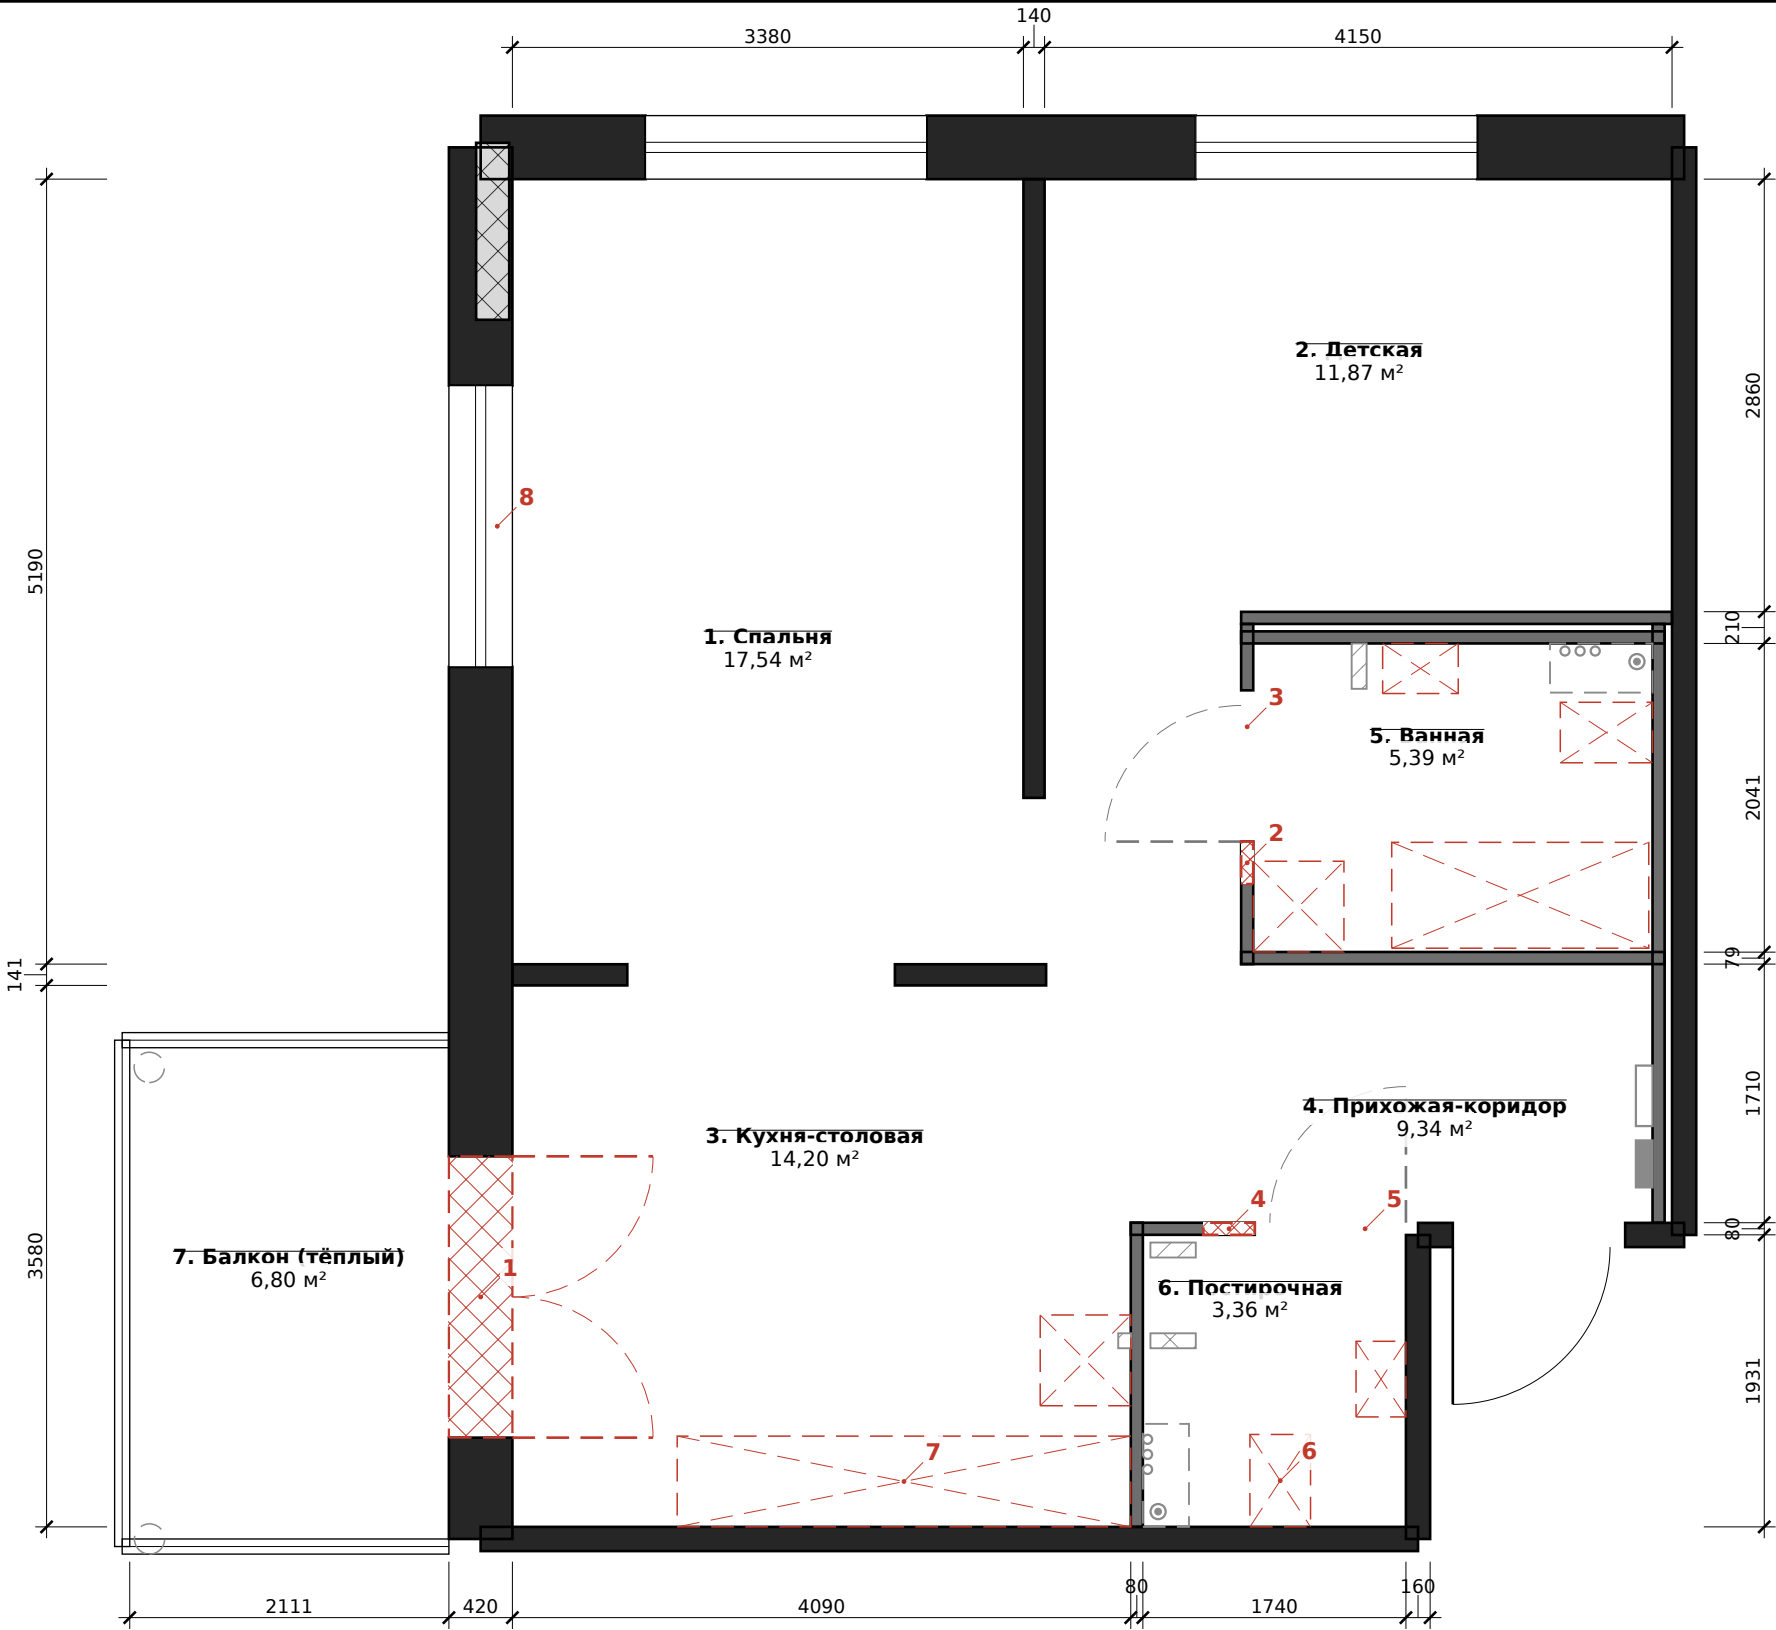

| Ведомость демонтажа |           |   |
|---------------------|-----------|---|
| Поз.                | Элемент   | Состав работ (planning.json)   |
| 1                   | O4-fill   | Демонтаж заполнения балконного проёма O4 (двустворчатый блок, порог) в границах проёма 1860; простенки, перемычка — сохраняются, проём не расширяется (D2)   |
| 2                   | W12-cut   | W12 (перегородка 80, ненесущая): пробивка участка у 4250..4531 под новую дверь ванной D3; разборка вручную, без ударного инструмента по стяжке   |
| 3                   | O7-part   | W12: закладка верхней части проёма O7 у 5050..5531 (NW8)   |
| 4                   | W11-cut   | W11 (перегородка 80): пробивка участка х 4570..4910 под новую дверь постирочной D4   |
| 5                   | O6-part   | W11: закладка части проёма O6 х 5370..5910 (NW9) — место пенала постирочной   |
| 6                   | F1        | Унитаз постирочной F1 (если установлен) — демонтаж; выпуск Ø110 используется через переход 110/50 для отвода СМА+хозмойки или заглушается с доступом (ревизия у U5); подводка ХВС к WC — заглушка у тройника с шаровым краном в зоне люка                                                                              |
| 7                   | F-all     | Прочие сантехприборы и кухня застройщика (F2-F8), если установлены — демонтаж с повторной установкой по проекту   |
| 8                   | O1-infill | Окно O1: демонтаж только подоконной доски и внутренних откосов (если есть); оконный блок и наружный слой стены НЕ трогаются   |
| 9                   | keep      | НЕ демонтируются: наружные стены W1, W2 (в т.ч. простенки 590/1130 и перемычка O4, оконные блоки O1/O2 — зашиваемое окно остаётся на месте), межквартирные/МОП W3-W6, W7, W8, колонна C1, W12 (кроме участка под дверь), W13-W16, коробка стояков U5/U10, вентканал U12 (сечение не уменьшать), коллекторы ТП U11/U14. |

- Условные обозначения
- Сохраняемые несущие/наружные стены
  - Сохраняемые перегородки
  - Демонтируемые участки стен / заполнения проёмов
  - Демонтируемые приборы и блоки (если установлены)
  - Существующие дверные блоки O6/O7 (проёмы изменяются, см. AP-06)

|          |        |            |       |       |         |                                   |                     |      |        |
|----------|--------|------------|-------|-------|---------|-----------------------------------|---------------------|------|--------|
|          |        |            |       |       |         | КВ108-ДП-АР-05                    |                     |      |        |
|          |        |            |       |       |         | Квартира №108, СПб, дизайн-проект |                     |      |        |
| Изм.     | Кол.уч | Лист       | №док. | Подп. | Дата    | Архитектурные решения             | Стадия              | Лист | Листов |
| Разраб.  |        | рпб-агенты |       |       | 10.2026 |                                   | Р                   | 9    | 39     |
| Пров.    |        |            |       |       |         | План демонтажа<br>Масштаб 1:50    | ПИБ<br>агенты рпб-* |      |        |
| ГИП      |        |            |       |       |         |                                   |                     |      |        |
| Н.контр. |        |            |       |       |         |                                   |                     |      |        |
| Утв.     |        |            |       |       |         |                                   |                     |      |        |