


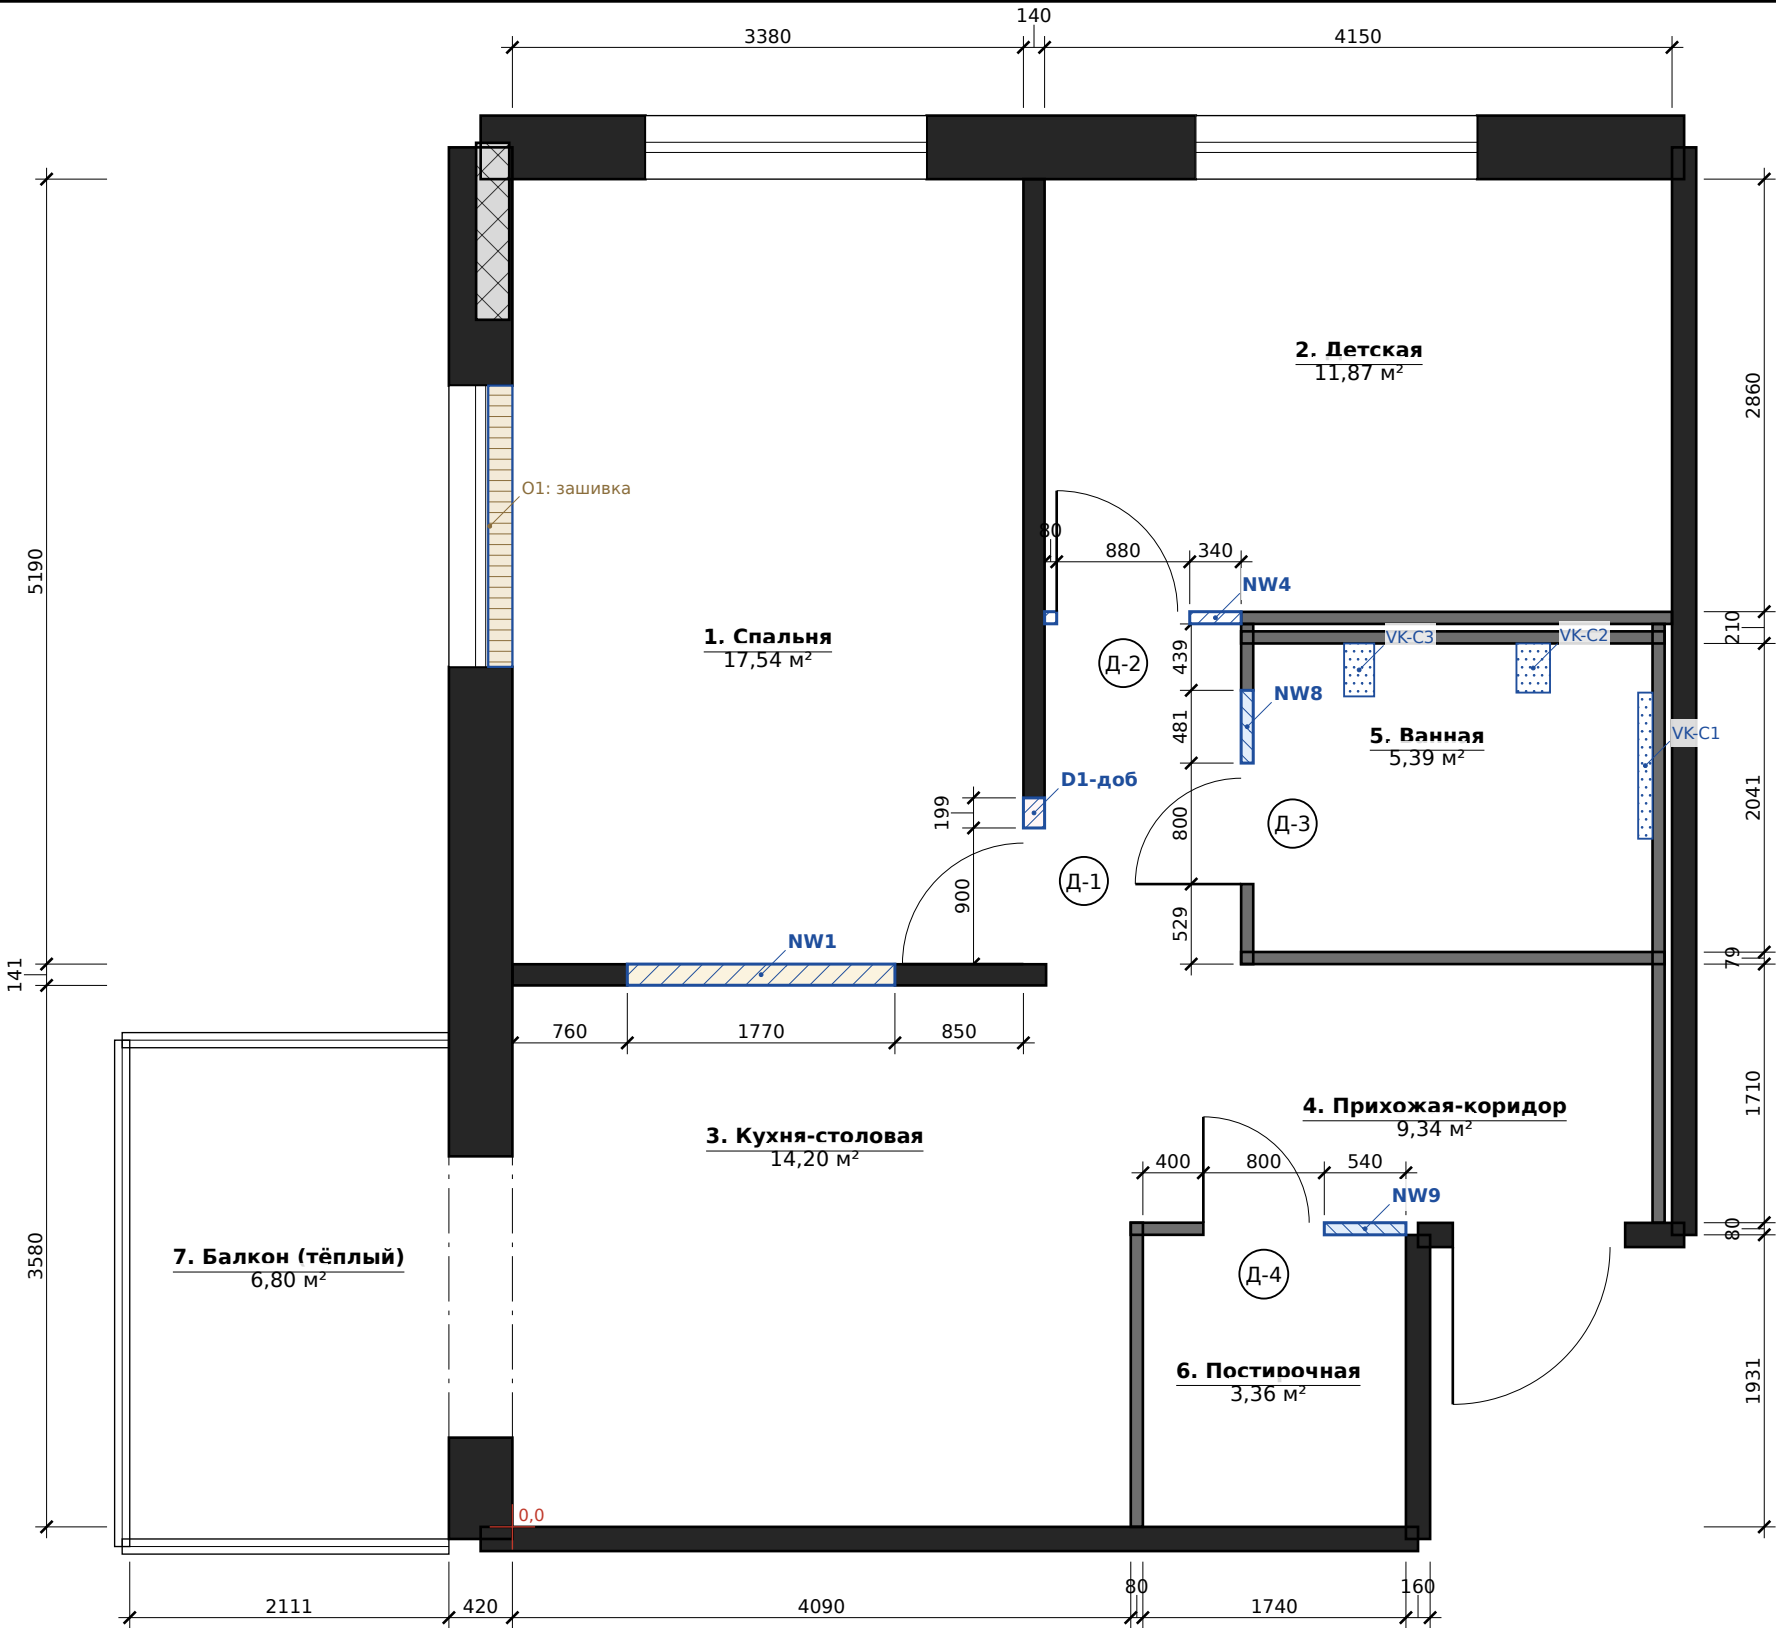

Ведомость перегородок и облицовок (мм)

Марка	t	L	L нетто	Материал	Назначение
NW1	140	1770	1770	ПГП 100 полнотелые + облицовка ГКЛ 12,5 на клею со стороны кухни (в плоскость простенков W8, 140 мм); акустическая лента по контуру; без перевязки с несущей W8 — гибкие анкеры к простенкам, к перекрытию — скобы	закладка проёма O9 (кухня/спальня) в плоскости несущей W8 — без изменения несущих элементов
NW4	80	1300	420	ПГП 80 полнотелые (гипсовые), на гипсовом клею по демпферной ленте, БЕЗ дюбелей в пол (водяной ТП, D3); крепление к стенам/потолку скобами	отделение комнаты 11,97 от коридора (в линию W16)
NW8	80	481	481	ПГП 80 гидрофобизированные (ПГП-Г), на клею по демпферной ленте, без дюбелей в пол; обмазочная гидроизоляция со стороны с/у	закладка верхней части O7 (дверь ванной смещается вниз)
NW9	80	540	540	ПГП 80 гидрофобизированные (ПГП-Г), на клею по демпферной ленте, без дюбелей в пол; обмазочная гидроизоляция со стороны с/у	закладка правой части O6 (место пенала постирочной)
D1-доб	140	199	199	ПГП (doors.json: «добор ПГП 199»)	добор в проёме O8 у двери D-1
VK-C1	95	966	—	каркас ПП 60/27 (или стальной 50) с отступом, 2хГВЛВ/ЦСП 12,5, гидроизоляция, плитка; итого ≈ 95 мм от W14; к W14 и потолку, БЕЗ крепления в пол (D3) — нижний профиль на клею по подиуму; высота — до потолка	Облицовка W14 в зоне душа (инсталляционная стенка)
VK-C2	222	325	—	ГКЛВ/ГВЛВ на каркасе, высота +450 от пола ванной, верх — полка; над ней открыт доступ к люку H1	Низкий короб-перемычка между коробом инсталляции и коробом U10
VK-C3	199	350	—	подиум +80 не заливать в зону коллектора: рамка из уголка/ЦСП, гидроизоляция с заведением на рамку, дно ниши — существующая стяжка; доступ через съёмный цоколь тумбы	Рамка-бортик вокруг коллектора ТП U14 в подиуме

Условные обозначения

- Сохраняемые несущие/наружные стены
- Сохраняемые перегородки
- ПГП 80 полнотелые (гипсовые) — новая перегородка
- ПГП-Г 80 гидрофобизированные (мокрые зоны)
- ПГП 100 + ГКЛ 12,5 (закладка проёма в плоскости несущей стены)
- Облицовка/короб ГКЛВ/ГВЛВ на каркасе
- Зашивка окна изнутри: каркас + утеплитель + пароизоляция + 2хГКЛ
- Добор ПГП в проёме O8 (no doors.json)

Указания по монтажу

- Водяной ТП в стяжке (D3): перегородки ПГП — на клею по демпферной ленте 10 мм, без дюбелей в пол; к стенам — гибкие связи/скобы, к перекрытию — скобы с дюбелями в плиту. Альтернатива — ГКЛ на металлокаркасе 75 + 2х12,5 (ГКЛВ в мокрых зонах), ПН к полу только на клею/ленте или дюбелями после схемы ТП и тепловизора.
- Перед монтажом — тепловизионная съёмка пола при работающем ТП, разметка трасс.
- Высота перегородок — до плиты (+2750), примыкание к потолку — упругое.
- Стены с/у (NW8, NW9) — ПГП-Г, гидроизоляция обмазочная с заходом 200, в душе — на высоту орошения.
- Зашивка окна — не перегородка: каркас в откосе + утеплитель + пароизоляция + 2хГКЛ + панель, съёмная (см. window_infill).

						КВ108-ДП-АР-06			
						Квартира №108, СПб, дизайн-проект			
Изм.	Кол.уч	Лист	№док.	Подп.	Дата	Архитектурные решения	Стадия	Лист	Листов
Разраб.		rib-агенты			10.2026		Р	10	39
Пров.									
ГИП						План монтажа перегородок Масштаб 1:50	ПИБ агенты rib-*		
Н.контр.									
Утв.									