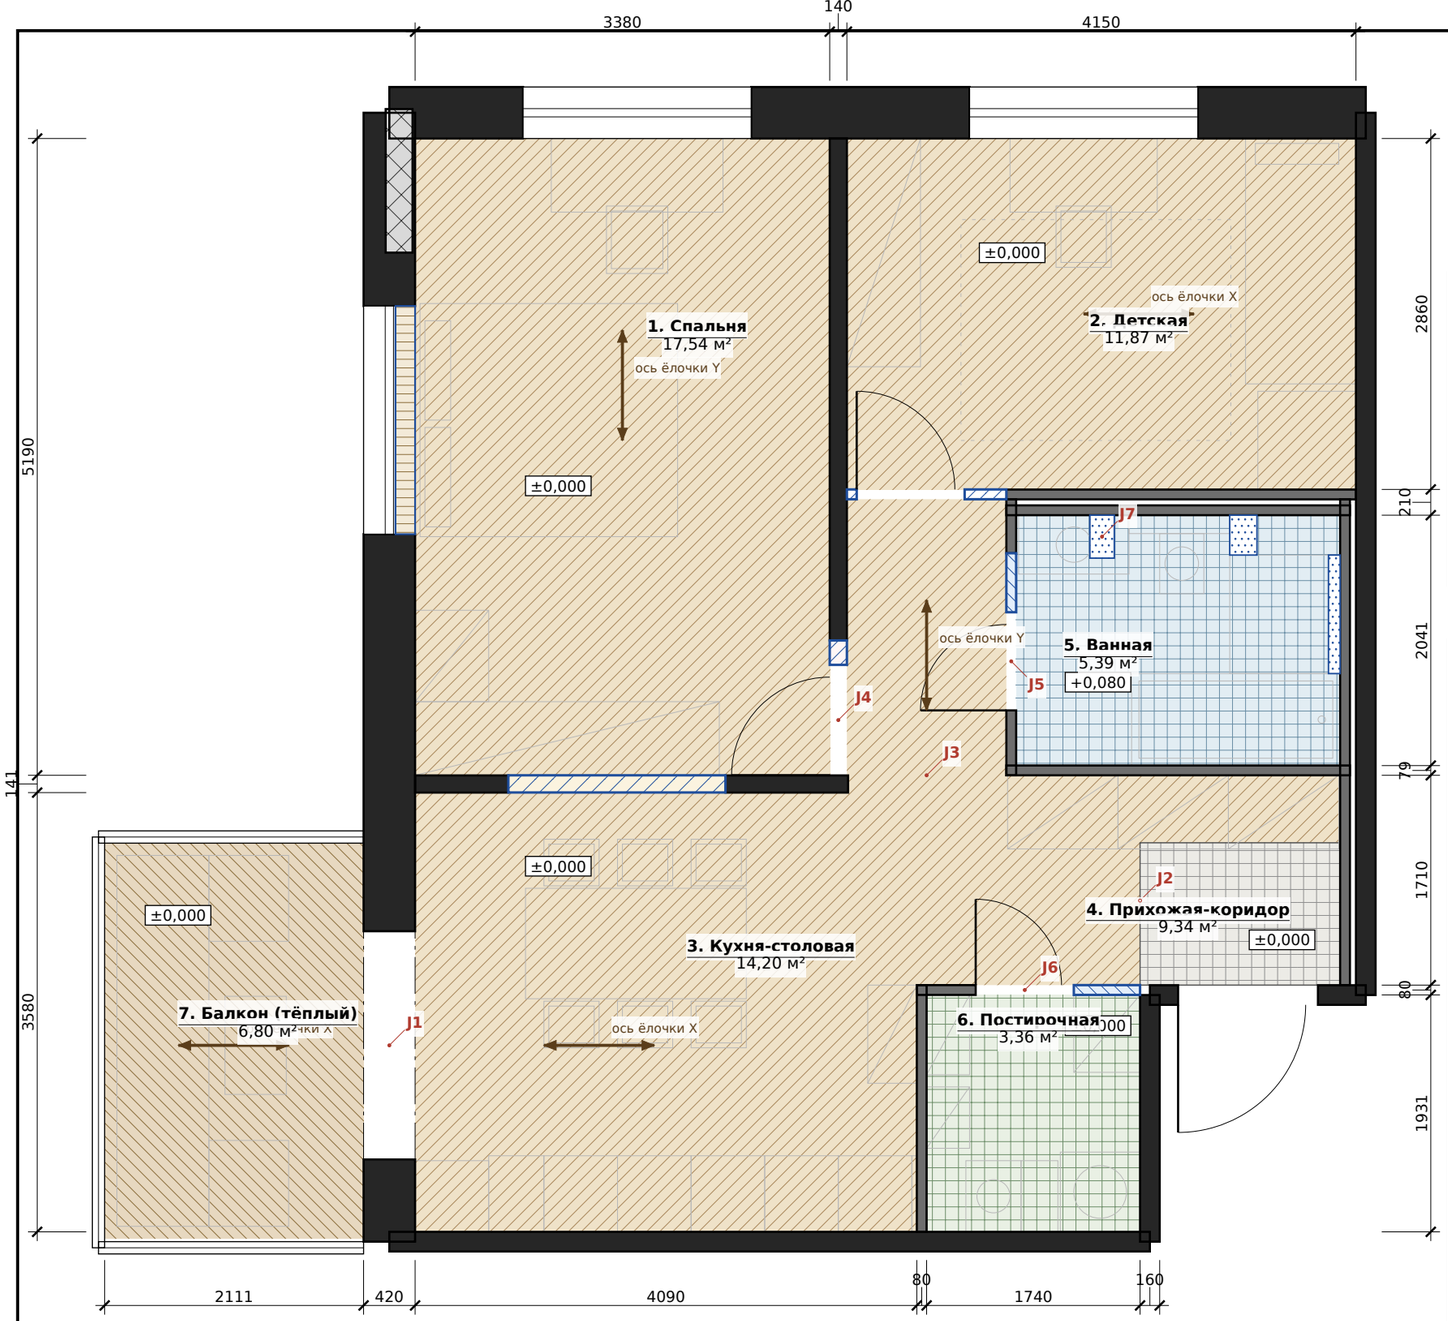


Условные обозначения

- M01 инж. доска дуб «ёлочка» (P-OAK)
- M16 керамогранит 600×600 у входа (P-TILE-HALL)
- M20 керамогранит, подиум +80 (P-BATH)
- M25 керамогранит 600×600 (P-LAUNDRY)
- M28 LVT «ёлочка» (P-BALC)
- J1 — Стык покрытий / порог (таблица ниже, узлы АР-17/18)

Ведомость покрытий

Пом.	Покрытие	Пирог	Отм.	Обогрев	Плинтус
R1	M01 инж. доска дуб ёлочка	P-OAK	±0,000	водяной (сущ.)	M02 МДФ h 120 C2, только к стене
R2	M01 ёлочка	P-OAK	±0,000	водяной (сущ.)	M02 h 120 C5
R3	M01 ёлочка	P-OAK	±0,000	водяной (сущ.)	M02 C2; за кухней — цоколь мебели
R4	M01 ёлочка + M16 керамогранит у входа	P-OAK / P-TILE-HALL	±0,000	водяной (сущ.)	M02 C2; у керамогранита — плинтус из керамогранита h 10…
R5	M20 керамогранит 60×60 / 60×120 R10/B (душ)	P-BATH	+0,080	электро TP1 1,89 м² (electrical.json), не под ванной/душем/коробами/U14	нет — плитка стен до пола, герметик
R6	M25 керамогранит 60×60 R10	P-LAUNDRY	±0,000	электро TP2 1,06 м², не под колонной/шкафами/U11	плитка/кромка шкафов
R7	M28 LVT клеевой ёлочка	P-BALC	±0,000	электро TP3 2,32 м² (свободный пол), t ≤ 27 °C	МДФ влагостойкий h 80 C6 по парапетам; П-диван на ножках

Пироги полов (floors.json)

Пирог	Слой (снизу вверх)	мм / отм.
P-OAK	**Инженерная доска дуб ёлочка на клею (M01) по стяжке с водяным ТП**	**верх 0**
	плита перекрытия (верх)	-100
	стяжка с водяным ТП застройщика (существующая, не трогать)	80
	грунт + локальный ремонтный состав (до 3)	3
	клей MS-полимер эластичный (зубчатый шпатель B11)	2
	инженерная доска 2-слойная 15 (90×600, ёлочка 1:6)	15
P-TILE-HALL	**Керамогранит 60×60 R10 у входа (M16)**	**верх 0**
	плита	-100
	стяжка с водяным ТП (сущ.)	80
	грунт, ремонтный состав	2
	клей C2TE S1 (эластичный, для ТП)	8
	керамогранит 600×600×10 ректификат	10
P-LAUNDRY	**Керамогранит 60×60 R10 + электро-ТП TP2 (M25)**	**верх 0**
	плита	-100
	стяжка с водяным ТП (сущ.)	80
	обмазочная гидроизоляция 2 слоя + ленты в углах, заход на стены 200	2
	клей C2TE S1 с нагревательным матом TP2 (мат 3 в слое клея)	8
	керамогранит 600×600×10	10
P-BATH	**Подиум ванной +80 (D18), керамогранит + электро-ТП TP1 (M20)**	**верх 80**
	плита	-100
	стяжка с водяным ТП (сущ.), верх −20 — не резать (D3/D4)	80
	грунт + нижняя обмазочная гидроизоляция (барьер над ТП и техподпольем), заход 200 над чистым полом	1.5
	демпферная лента 10 по периметру; трубы Ø50 трапа/ванны — на стяжке, защитный слой ≥ 30	0
	подиум ЦПС M300 фиброармированная + сетка 50×50 Bp4; в душе уклон 1,5 % к трапу	78.5
	основная обмазочная гидроизоляция 2 слоя, ленты, манжета/фланец трапа, вклейка в рамку U14	2
	клей C2TE S1 + мат TP1 (вне ванны, душа, коробов; ≥ 100 от рамки U14)	8
	керамогранит 10 (60×60 сухая зона, 60×120 душ R10/B)	10
P-BALC	**Пол балкона до ±0.000 (D1, D17, D22): утепление + стяжка + электро-ТП TP3 + LVT (M28)**	**верх 0**
	плита балкона [ДОПУЩЕНИЕ №46]	-120
	грунт, ремонт плиты, выравнивание перепадов > 5	0
	XPS 300 кПа 50 (швы проклеены), по периметру — XPS 20 на парапет	50
	плёнка ПЭ 200 мкм (пароизоляция, нахлёст 100, завод на стены 100) + демпферная лента 10	0
	стяжка ЦПС M300 фибра + сетка Bp4 50×50 (плавающая)	55
	нагревательный мат TP3 (только свободный пол) в самовыравнивающей смеси, ≥ 5 над матом	10

Пироги полов (floors.json) (продолжение)

Пирог	Слой (снизу вверх)	мм / отм.
	грунт + клей для LVT (дисперсионный, допуск ТП)	**0.5**
	LVT клеевой ёлочка 4,5 (слой износа ≥ 0,55)	4.5

Стыки и пороги

Стык	Где	Решение
J1	кухня/балкон, портал O4: x=−210 (ось стены), y 590..2450	Узел 7 (details.md): заподлицо, пробковый компенсатор 5 + латунный Т-профиль 8 на клею (без саморезов в пол)
J2	прихожая: x=5910 (y 2011..3171) и y=3171 (x 5910..7541)	Узел 4: заподлицо, пробка 5 + латунная вставка 3
J3	коридор/прихожая y=3721, x 3520..4820	фриз 2×90 заподлицо, без компенсатора
J4	двери D1 (x 3450, y 3721..4621) и D2 (y 6011, x 3600..4480)	шов-компенсатор пробка 5 под плоскостью полотна; без порога; подрез полотна 20 (K-14)
J5	дверь D3, W12 x 4820..4900, y 4250..5050	Узел 5: порог-ступень из керамогранита C9 (массив/ступень 20 мм + опорный ЦПС), верх +90 = пол ванной +10 (ограничитель воды); ступень 90 из коридора с контрастной фаской; гидроизоляция заведена на порог и под коробку; пандус НЕ делается (уклон к двери вывел бы воду в коридор) — D20
J6	дверь D4, W11 x 4570..5370	порог-ограничитель керамогранит/камень 15 со скруглёнными кромками, на клею; гидроизоляция заведена под порог
J7	рамка U14 в ванной x 5501..5700, y 5491..5841 (VK-C3, K-05)	Узел 6: бортик из ЦСП 20/нерж. уголка, верх +100 (на 20 выше пола ванной), гидроизоляция с подиума заведена на бортик и внутрь до дна ниши; облицовка бортика плиткой; съёмный цоколь F71 перед нишей

Изм.	Кол.уч	Лист	№док.	Подп.	Дата
Разраб.		pib-агенты			10.2026
Пров.					
ГИП					
Н.контр.					
Утв.					

KB108-ДП-АР-10

Квартира №108, СПб, дизайн-проект

Архитектурные решения

Стадия	Лист	Листов
Р	14	39

План полов
Масштаб 1:50

ПИБ
агенты pib-*

Формат А3