


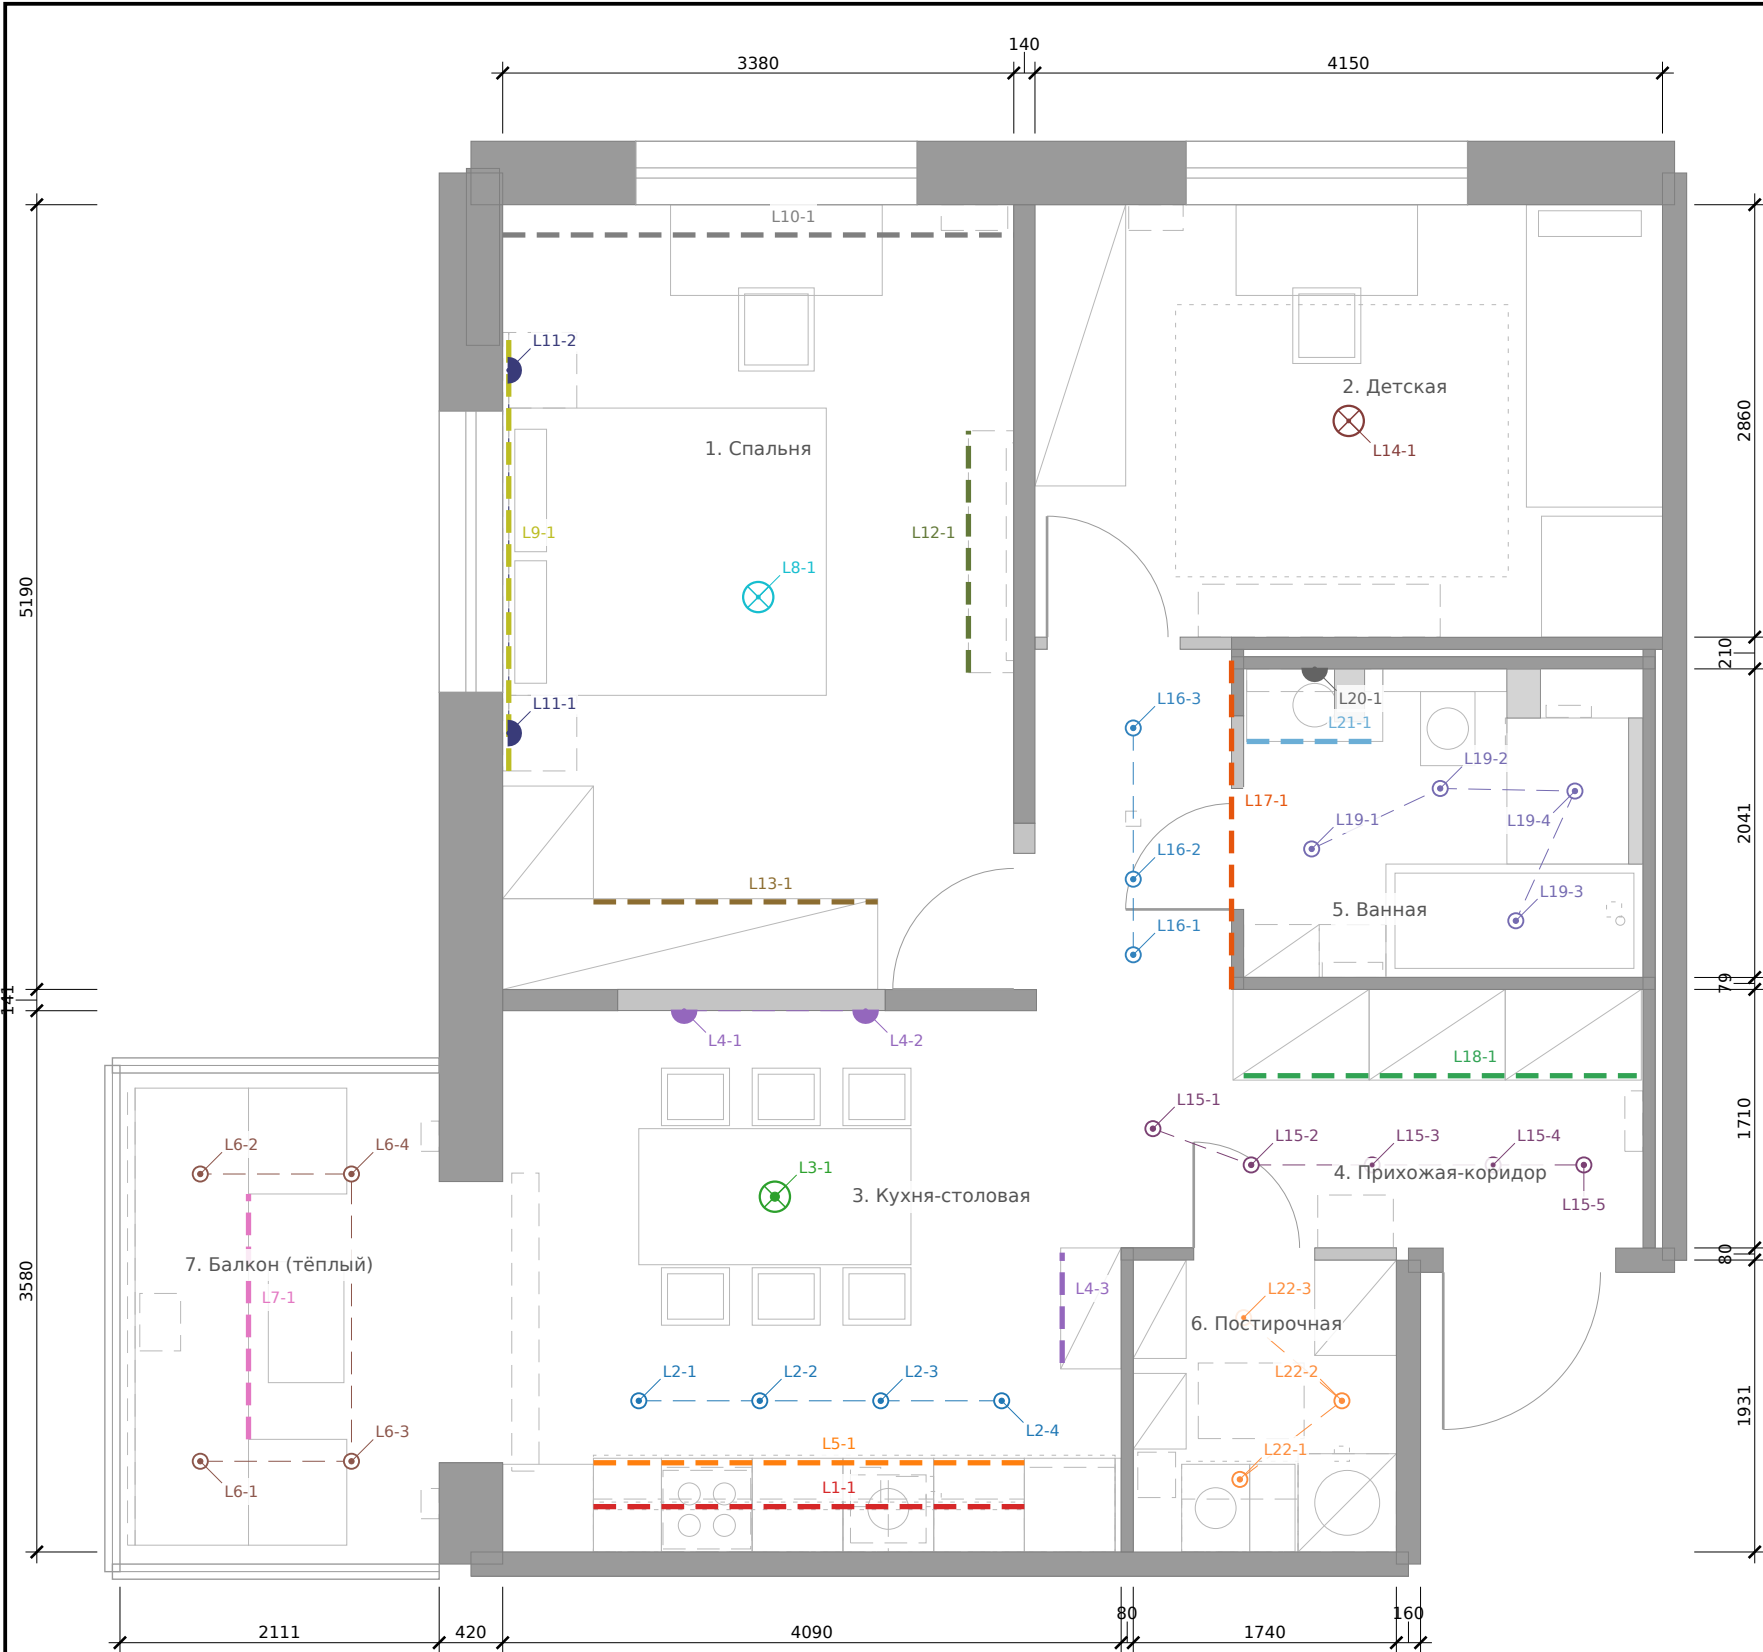

Основные обозначения (ГОСТ 21.614, ГОСТ 21.607)

- Светильник встраиваемый точечный (спот)
- Светильник потолочный (люстра, плафон)
- Светильник подвесной
- Светильник настенный (бра)
- Светодиодная лента (начало-конец по electrical.json)
- Связь светильников одной группы управления

Группы освещения

Группа	Назначение	Линия	Р, Вт
L1	Кухня — рабочая подсветка	C1	60
L2	Кухня — споты	C1	28
L3	Столовая — люстра	C1	40
L4	Столовая — бра + буфет	C1	22
L5	Кухня — цоколь (ночь/кино)	C1	15
L6	Балкон — споты	C1	20
L7	Балкон — цоколь дивана	C1	20
L8	Спальня — люстра	C2	40
L9	Спальня — LED буазери	C2	30
L10	Спальня — LED карниз	C2	55
L11	Спальня — бра	C2	10
L12	Спальня — консоль ТВ (ночник)	C2	10
L13	Спальня — шкаф-купе	C2	20
L14	Детская — потолочный	C2	40
L15	Прихожая — споты	C3	30
L16	Коридор — споты	C3	18
L17	Коридор — ночной плинтус	C3	15
L18	Прихожая — шкаф	C3	20
L19	Ванная — споты + вентилятор	C3	24
L20	Ванная — зеркальный шкаф	C3	15
L21	Ванная — ночник	C3	5
L22	Постирочная — споты + вентилятор	C3	18

Ведомость светильников

Марка	Пом.	Тип	Р,Вт	h	IP	K	Привязка, мм	Примечание
L1-1	R3	led_strip	60	1540	IP20	2700	600,300 → 3450,300	подсветка рабочей зоны под KW-01.05, 24 В, 2700К CRI>90 (F23); БП 60 Вт в карнизе над KW-01 (вывод P-K10)
L2-1	R3	spot	7	2650	IP20	2700	900 от W2; 1000 от W3	встраиваемый спот (глубина ≤ 80, пленум 87.5 — потолок кухни +2650, D19), над проходом у фронта кухни
L2-2	R3	spot	7	2650	IP20	2700	1700 от W2; 1000 от W3	встраиваемый спот (глубина ≤ 80, пленум 87.5 — потолок кухни +2650, D19), над проходом у фронта кухни
L2-3	R3	spot	7	2650	IP20	2700	1590 от W10; 1000 от W3	встраиваемый спот (глубина ≤ 80, пленум 87.5 — потолок кухни +2650, D19), над проходом у фронта кухни
L2-4	R3	spot	7	2650	IP20	2700	790 от W10; 1000 от W3	встраиваемый спот (глубина ≤ 80, пленум 87.5 — потолок кухни +2650, D19), над проходом у фронта кухни
L3-1	R3	pendant	40	1600	IP20	2700	1800 от W2; 1230 от NW1	люстра столовой по оси стола F25 (латуны/ткань, 5-6 рожков LED), низ +1600 (= 840 над столом), диммер
L4-1	R3	wall	6	1650	IP20	2700	1200 от W2; 0 от NW1	бра столовой на NW1 (рамки M14), латунь
L4-2	R3	wall	6	1650	IP20	2700	2400 от W2; 0 от NW1	бра столовой на NW1
L4-3	R3	led_strip	10	1900	IP20	2700	3700,1250 → 3700,1980	LED остеклённого яруса буфета F24, 24 В, БП на крыше буфета (вывод P-K12)
L5-1	R3	led_strip	15	80	IP20	2700	600,590 → 3450,590	подсветка цоколя кухни 2700К (сцены «Кино» 5 %, «Ночь»), БП за съёмным цоколем K-04 (вывод P-K11)
L6-1	R7	spot	5	2500	IP20	2700	531 от B1; 680 от B3	малый спот по периметру (M30), в толще ГКЛВ по утеплителю; вне луча проектора
L6-2	R7	spot	5	2500	IP20	2700	531 от B1; 668 от B2	малый спот по периметру (M30), в толще ГКЛВ по утеплителю; вне луча проектора
L6-3	R7	spot	5	2500	IP20	2700	580 от W2; 680 от B3	малый спот по периметру (M30), в толще ГКЛВ по утеплителю; вне луча проектора
L6-4	R7	spot	5	2500	IP20	2700	580 от W2; 668 от B2	малый спот по периметру (M30), в толще ГКЛВ по утеплителю; вне луча проектора
L7-1	R7	led_strip	20	100	IP20	2700	-1681,745 → -1681,2368	подсветка цоколя П-дивана 24 В 2700К (F33), Zigbee-контроллер 24 В, БП в отсеке AV F35 (вывод P-B05)
L8-1	R1	ceiling	40	2700	IP20	2700	1690 от W2; 2595 от NW1	потолочная люстра (центр комнаты), диммируемая
L9-1	R1	led_strip	30	2650	IP20	2700	40,5166 → 40,8066	LED 2700K в теновом пазу карниза буазери F41; БП 24 В в съёмном ящике у карниза (вывод P-R10)
L10-1	R1	led_strip	55	2650	IP20	2700	0,8711 → 3380,8711	LED 2700K в карнизе по кромке ниши шторы CN-1 (у 8711, clashes F-06) и по W7, БП у W7 (вывод P-R11)
L11-1	R1	wall	5	1150	IP20	2700	40 от W2; 1696 от W8	бра у изголовья (сторона входа), латунь + абажур
L11-2	R1	wall	5	1150	IP20	2700	40 от W2; 1095 от W1	бра у изголовья (сторона окна)
L12-1	R1	led_strip	10	250	IP20	2700	3080,5816 → 3080,7416	подсветка снизу ТВ-консоли F47 2700К (ночной свет 5 % по датчику движения); БП в консоли (вывод P-R12)
L13-1	R1	led_strip	20	2500	IP20	2700	600,4300 → 2480,4300	подсветка шкафа-купе F45 по датчикам открытия; БП на антресоли (вывод P-R13, без выключателя)
L14-1	R2	ceiling	40	2700	IP20	2700	2075 от W7; 1430 от W1	потолочный рассеянный светильник, Zigbee-диммер в коробке выключателя (пульт у кровати)
L15-1	R4	spot	6	2650	IP20	2700	3241 от W14; 789 от W11	спот прихожей (потолок +2650, D19)
L15-2	R4	spot	6	2650	IP20	2700	2591 от W14; 549 от W11	спот прихожей (потолок +2650, D19)
L15-3	R4	spot	6	2650	IP20	2700	1791 от W14; 549 от NW9	спот прихожей (потолок +2650, D19)
L15-4	R4	spot	6	2650	IP20	2700	991 от W14; 550 от W5	спот прихожей (потолок +2650, D19)
L15-5	R4	spot	6	2650	IP20	2700	391 от W14; 550 от W5	спот прихожей (потолок +2650, D19)
L16-1	R4	spot	6	2650	IP20	2700	650 от W7; 1939 от W10	спот коридора (потолок +2650, D19)
L16-2	R4	spot	6	2650	IP20	2700	650 от W7; 1521 от NW4	спот коридора (потолок +2650, D19)
L16-3	R4	spot	6	2650	IP20	2700	650 от W7; 521 от NW4	спот коридора (потолок +2650, D19)
L17-1	R4	led_strip	15	50	IP20	2700	4820,3721 → 4820,5971	ночная подсветка в плинтусе коридора/прихожей по датчикам движения 5-10 % (сценар: «Ночь»); БП 24 В на антресоли F60 (...)
L18-1	R4	led_strip	20	2500	IP20	2700	4900,3150 → 7500,3150	подсветка шкафа прихожей F60-F62 по датчикам открытия; БП на антресоли F61 (вывод P-H04)
L19-1	R5	spot	6	2370*	IP44	3000	450 от W12; 849 от W13	спот IP44, вне зон 0-1
L19-2	R5	spot	6	2370*	IP44	3000	1246 от VK-C1; 791 от W15	спот IP44 над WC
L19-3	R5	spot	6	2370*	IP65	3000	841 от W14; 374 от W13	спот IP65 над ванной (потолок ГКЛВ +2450 от УЧП = 2370 от пола ванной > 2250 — вне зоны 1)
L19-4	R5	spot	6	2370*	IP65	3000	355 от VK-C1; 808 от W15	спот IP65 над душем
L20-1	R5	wall	15	1950*	IP44	3000	131 от VK-C3; 0 от W15	LED зеркального шкафа F72 (встроенный сенсорный выключатель), вывод P-B3 h=1950 без коммутации
L21-1	R5	led_strip	5	450*	IP67	3000	4920,5361 → 5820,5361	ночная подсветка под тумбой F71 по датчику движения, SELV 12 В; БП 12 В в верхнем отсеке зеркального шкафа (вне зон)
L22-1	R6	spot	6	2500	IP44	3000	705 от W10; 480 от W3	спот IP44 в подшивном потолке +2500 (hvac.json), вне сушилки F89
L22-2	R6	spot	6	2500	IP44	3000	360 от W4; 931 от NW9	спот IP44 в подшивном потолке +2500 (hvac.json), вне сушилки F89
L22-3	R6	spot	6	2500	IP44	3000	730 от W10; 381 от W11	спот IP44 в подшивном потолке +2500 (hvac.json), вне сушилки F89

Примечания

Высоты h — до центра изделия от УЧП ±0.000; привязки — до грани ближайшей стены по X и по Y, мм.
* В ванной R5 высоты — от чистого пола ванной (+80 к УЧП квартиры).
Водяной ТП в стычке, шпатель пол и крепить в пол ЗАПРЕЩЕНО. Все кабели — по потолку в гофре ПВХ нг Ø16-25 в зазоре 50 мм между чистовым потолком (ГКЛ/натяжной, +2700) и плитой (+2750), в коридоре/слу — в коробах +2450, 2500; спуски к точкам — вертикальными штробами (кирпич — ≤ 25 мм, только вертикально; ж/б — без штроб, облицовка ГКЛ/накладной монтаж); горизонтальные участки на стенах — только у потолка (в зоне 150 мм) или в плинтусе-кабель-канале (под окнами О2/О3, мебель балкона). Штробы в плите перекрытия — не применяются. Кабели на балконе — через откосы проёма О4 (без сверления перемычки и простенков). Разводка лучами из щита/шлейфом через подрозетники; распаечные коробки — только доступные (у люков/за светильниками)

КВ108-ДП-ЭО-01

Квартира №108, СПб, дизайн-проект

Изм.	Кол.уч	Лист	№док.	Подп.	Дата	Электросвешение	Стадия	Лист	Листов
Разраб.		rib-агенты			10.2026		Р	25	39
Пров.									
ГИП									
Н.контр.						План освещения Масштаб 1:50		ПИБ агенты rib-*	
Утв.									